

93 011001018229510711dfl

ТФРП.401.362281.01.00110

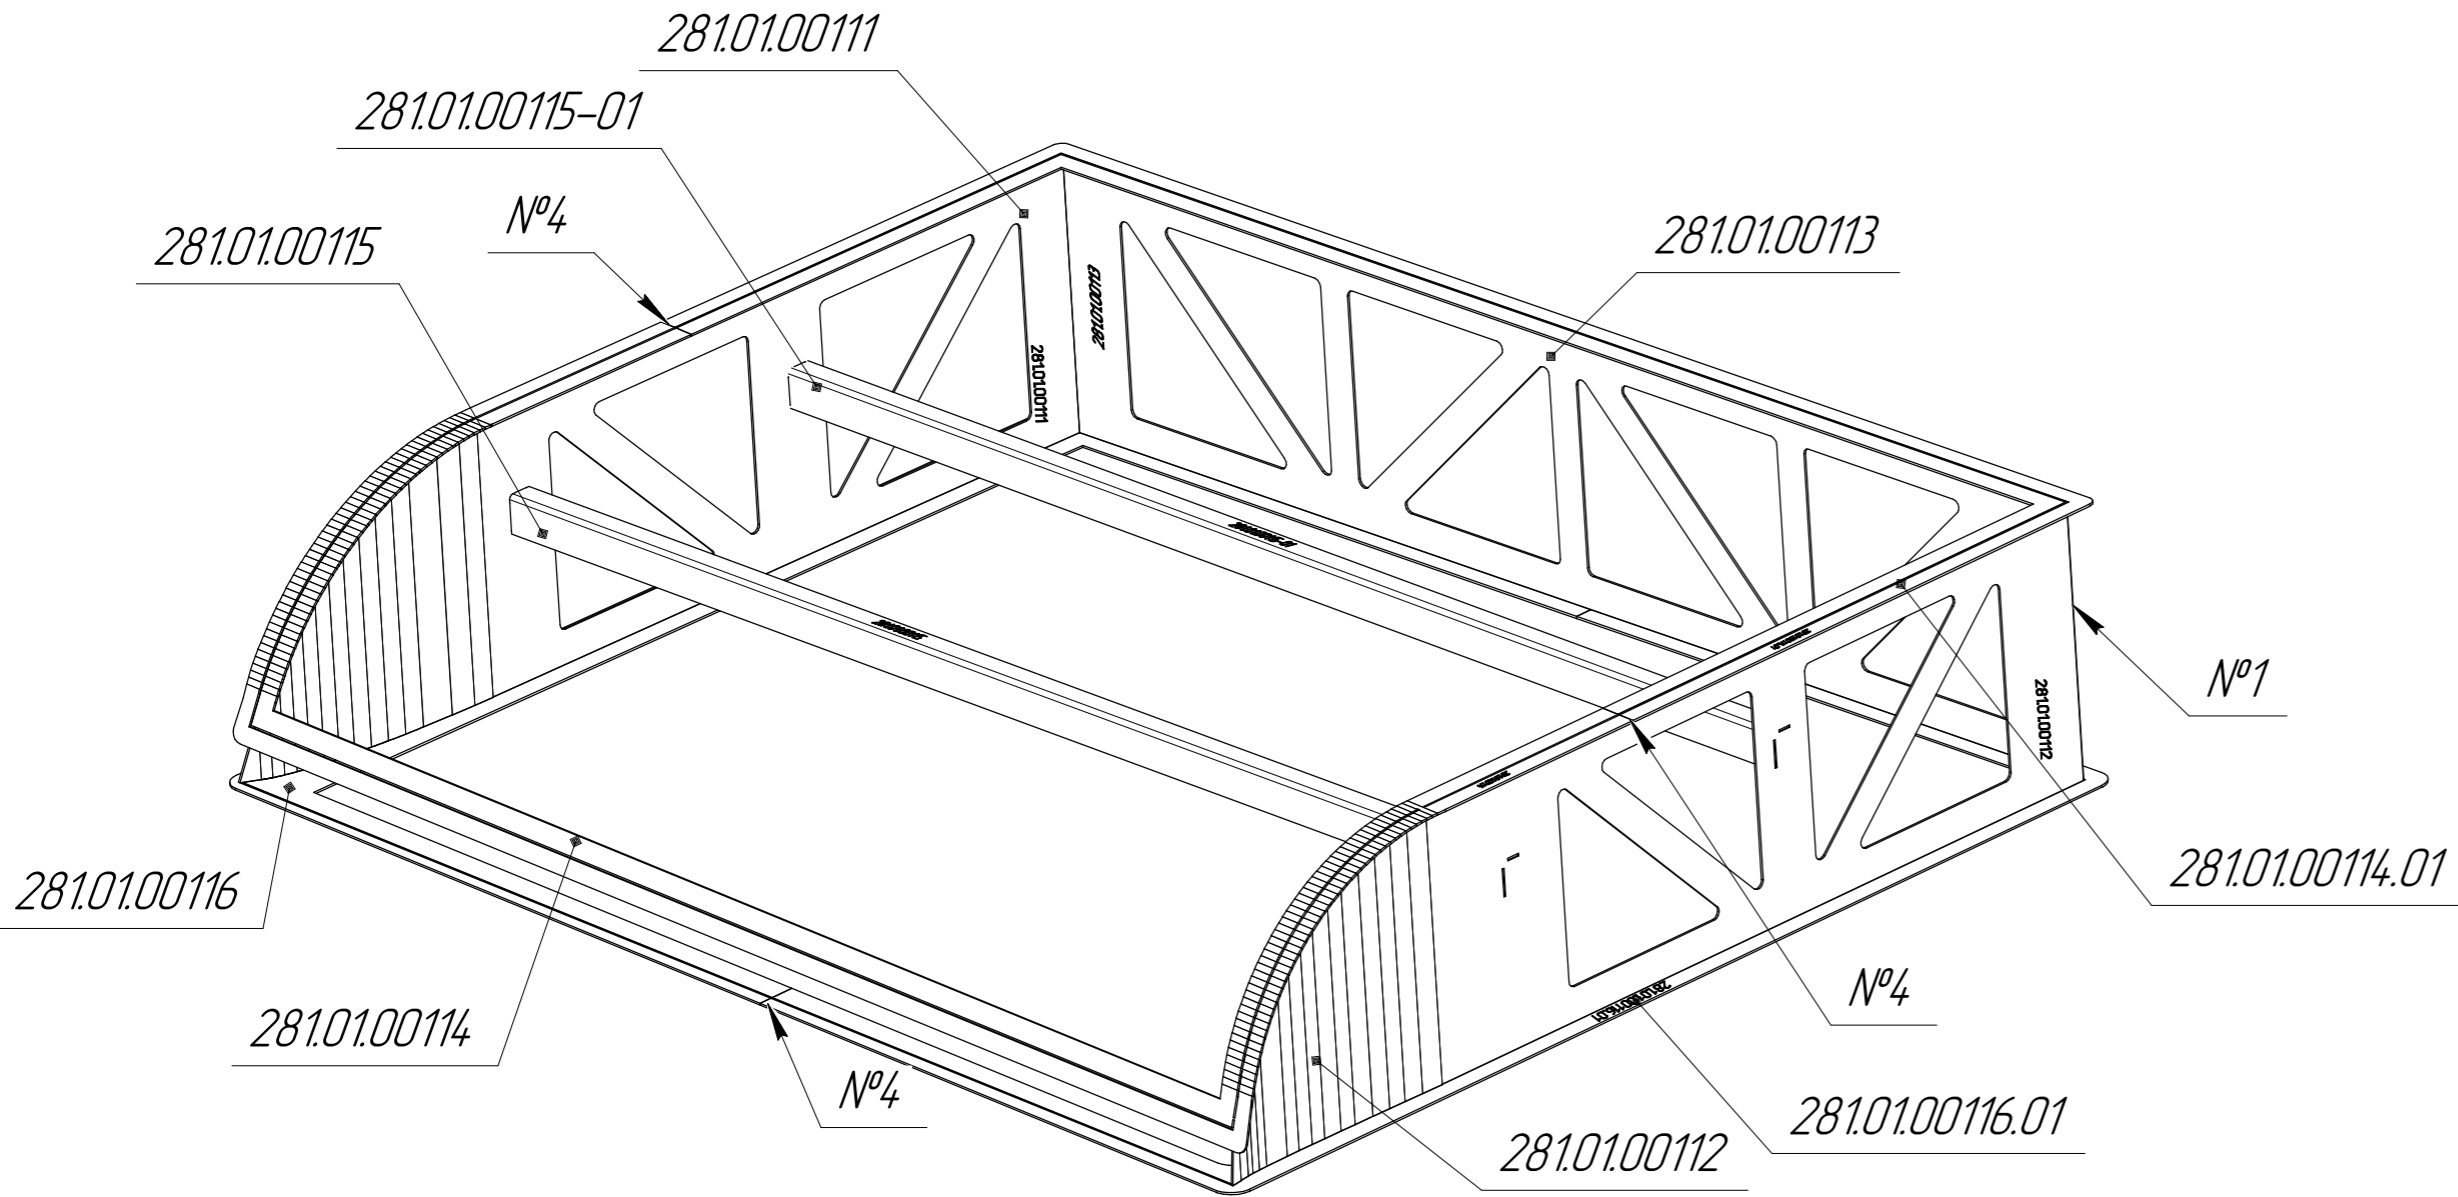



Таблица сварных швов

				<i>S</i>	<i>S</i> <sub>1</sub>	<i>b</i>		<i>e</i>	<i>e</i> <sub>1</sub>	<i>g</i>	<i>K</i>	
						Номин.	Пред. откл.					
№1	У4			3	3	0	+1			1±0.5		ГОСТ 14 771-76
№2	ТЗ-К-50z100			3	3						4+3	ГОСТ 14 771-76
№3	Т1			3	3						4+3	ГОСТ 14 771-76
№4	С7			3	4						4+3	ГОСТ 14 771-76





Выполнить сборку в следующем порядке:

1. Варить ТФРП.401.362281.01.00116 к ТФРП.401.362281.01.00116.01 и ТФРП.401.362281.01.00114 к ТФРП.401.362281.01.00114.01 стыковым швом С7
2. Варить ТФРП.401.362281.01.00115 и ТФРП.401.362281.01.00115-01 к ТФРП.401.362281.01.00111 внутри швом Т1, снаружи варить через пазы.
3. Приварить ТФРП.401.362281.01.00112, ТФРП.401.362281.01.00113 угловым швом У4
4. Установить по гравировке на ТФРП.401.362281.01.00116 и ТФРП.401.362281.01.00116.01. Варить шахматным швом Т3
5. Приварить ТФРП.401.362281.01.00114 и ТФРП.401.362281.01.00114.01 гравировкой вверх шахматным швом Т3

Формат	Зона	Поз.	Обозначение	Наименование	Кол.	Примечание	
			Переменные данные для исполнений:				
				ТФРП.401.362281.01.00110			
			Детали				
*)	1		ТФРП.401.362281.01.00111	Стенка 1	1	*12хА3	
*)	2		ТФРП.401.362281.01.00112	Стенка 2	1	*12хА4	
	3		ТФРП.401.362281.01.00113	Стенка 3	1		
*)	4		ТФРП.401.362281.01.00114	Обечайка верхняя	1	*12хА4	
*)	5		ТФРП.401.362281.01.00114.01	Обечайка верхняя	1	*12хА4	
*)	6		ТФРП.401.362281.01.00115	Уголок	1	*12хА4	
*)	7		ТФРП.401.362281.01.00115-01	Уголок	1	*12хА4	
*)	8		ТФРП.401.362281.01.00116	Фланец	1	*12хА4	
*)	9		ТФРП.401.362281.01.00116.01	Фланец	1	*12хА4	
				ТФРП.401.362281.01.00110-1			
			Детали				
*)	4		ТФРП.401.362281.01.00114-01	Обечайка верхняя	1	*12хА4	
*)	5		ТФРП.401.362281.01.00114.01-01	Обечайка верхняя	1	*12хА4	
*)	6		ТФРП.401.362281.01.00115-02	Уголок	1	*12хА4	
*)	8		ТФРП.401.362281.01.00116-01	Фланец	1	*12хА4	
*)	9		ТФРП.401.362281.01.00116.01-01	Фланец	2	*12хА4	
	10		ТФРП.401.362281.01.00111-01	Стенка 1	1		
	11		ТФРП.401.362281.01.00112-01	Стенка 2	1		
	12		ТФРП.401.362281.01.00113-01	Стенка 3	1		
	13		ТФРП.401.362281.01.00115-03	Уголок	1		
			ТФРП.401.362281.01.00110 СБ				
Изм.	Лист	№ докум.	Подп.	Дата	Оснастка стекла 11 Сборочный чертеж		
Разраб.		Ахметова					
Пров.							
Т.контр.							
Н.контр.							
Утв.							
					Лит.	Масса	Масштаб
						57,61	1:10
					Лист	1	Листов 3
					Копировал		
					Формат А2		

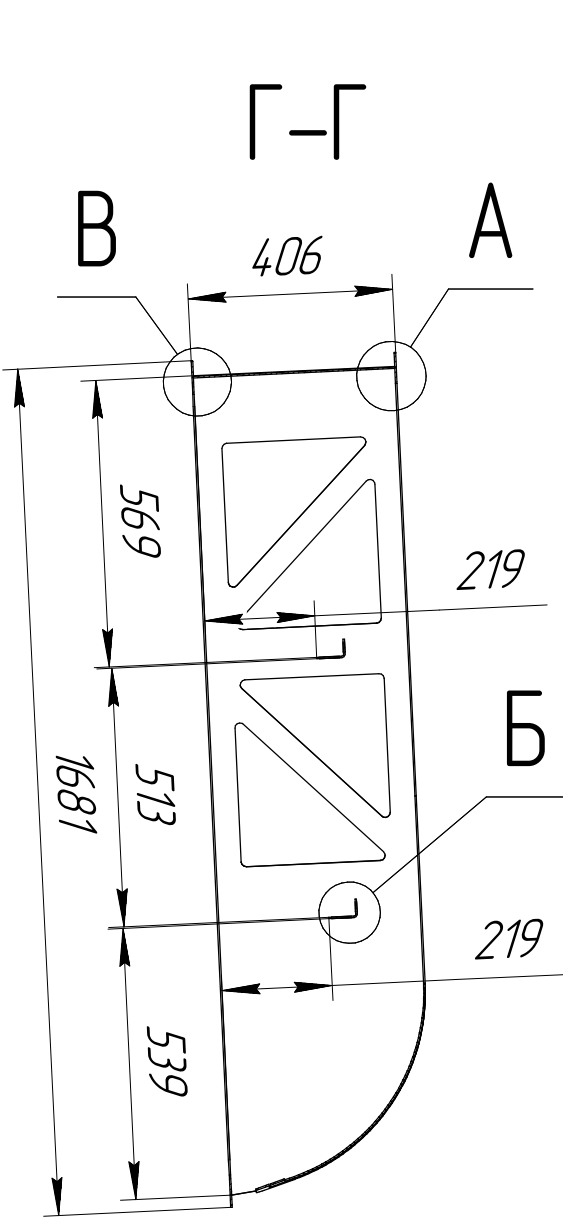

Выдержать размер по гравировке

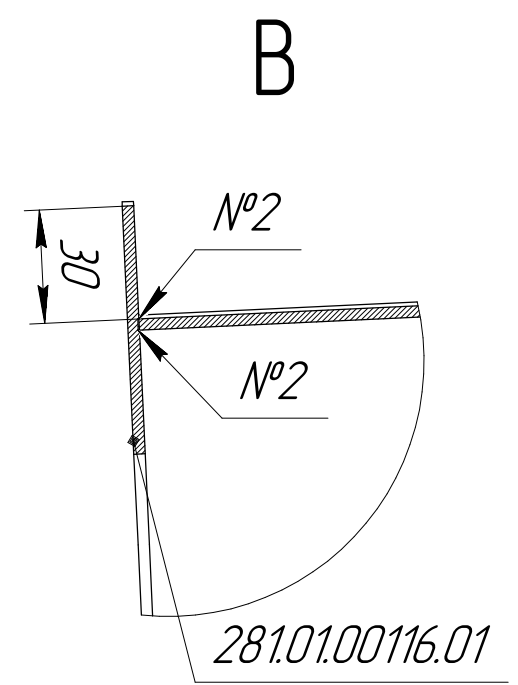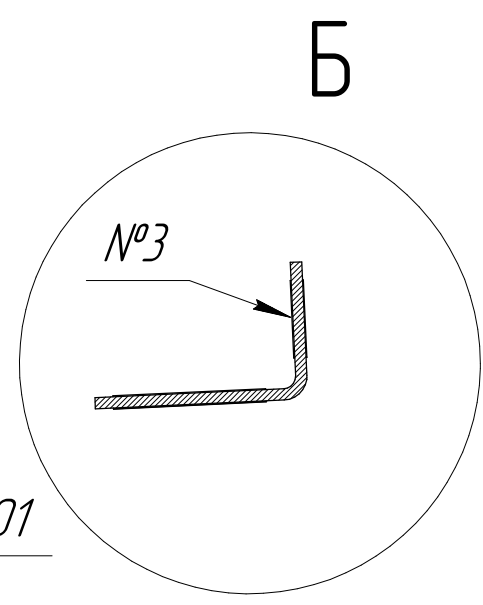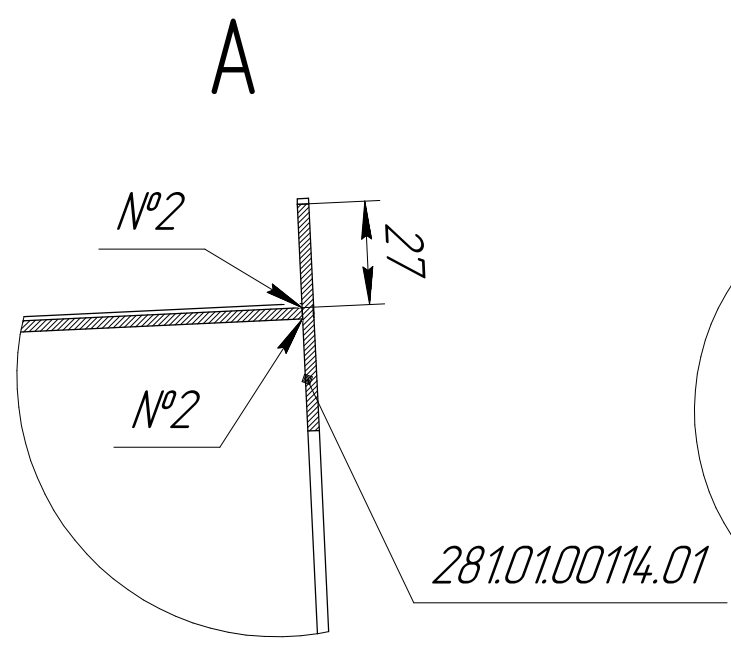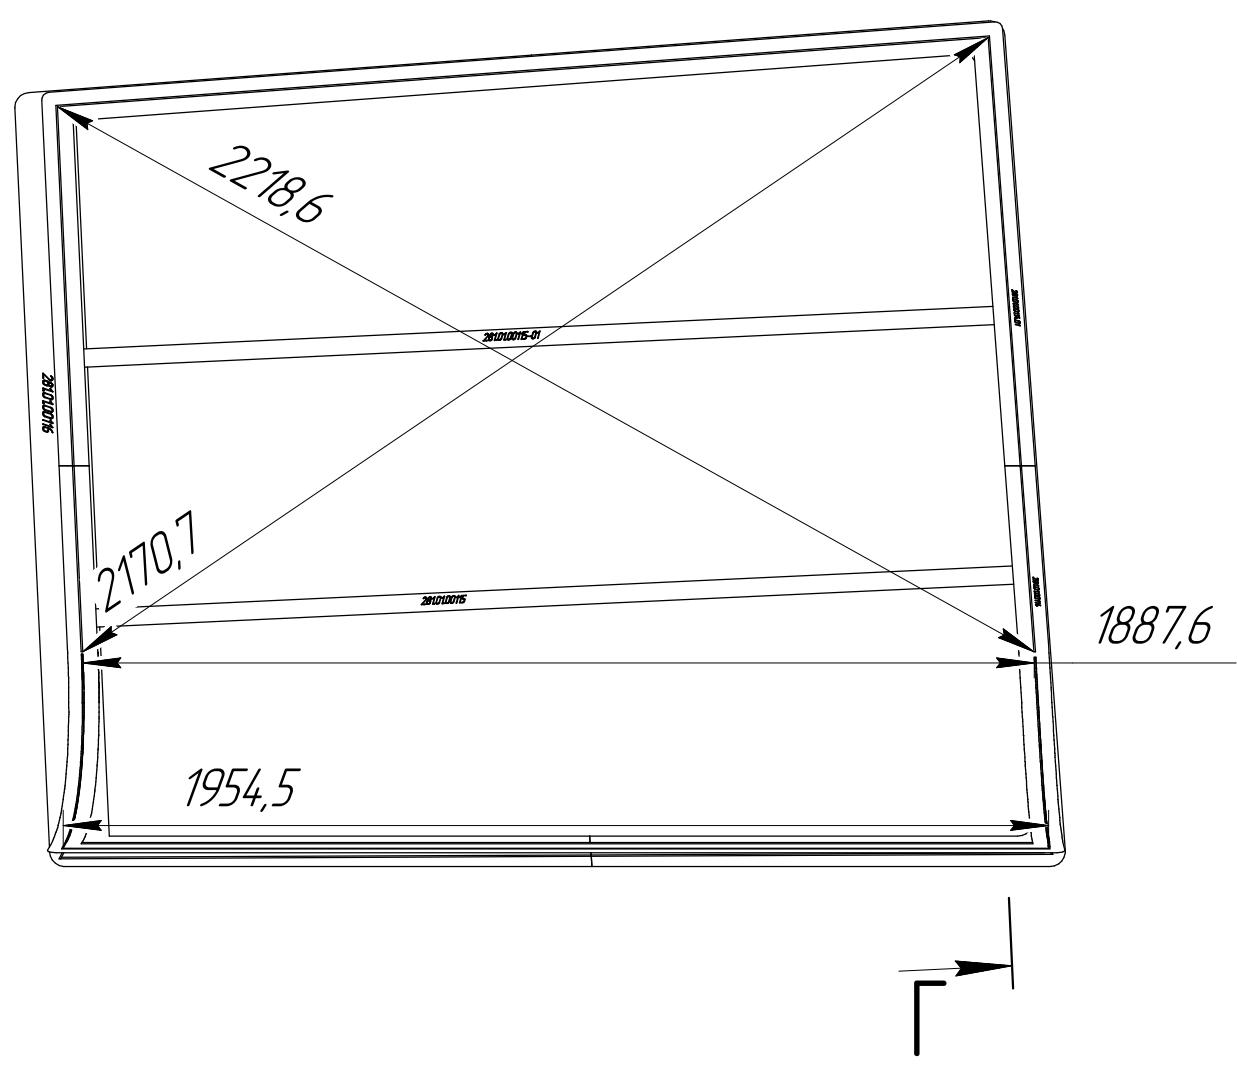


Инв. № подл.	Подп. и дата	Взам. инв. №	Инв. № дубл.	Подп. и дата

Изм.	Лист	№ докум.	Подп.	Дата

ТФРП.401.362281.01.00110 СБ

ТФРП.401.362281.01.00110-01 – зеркальное отражение  
Остальное – см. ТФРП.401.362281.01.00110

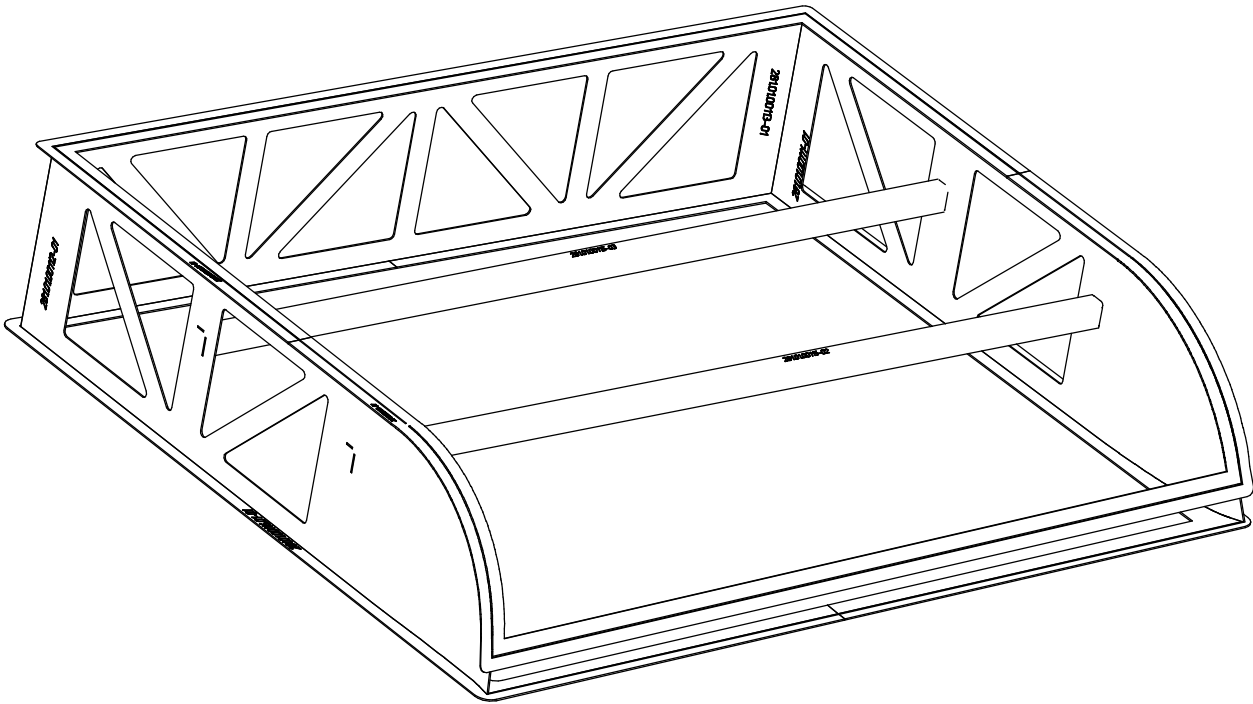

Инв. № подл.	Подл. и дата	Взам. инв. №	Инв. № дудл	Подп. и дата

Изм.	Лист	№ докум.	Подп.	Дата

ТФРП.401.362281.01.00110 СБ

Копировал

Формат А3