



Инв. № подл.					Подп. и дата	Взам. инв. №	Инв. № дубл.	Подп. и дата	
--------------	--	--	--	--	--------------	--------------	--------------	--------------	--	--	

Справ. №		Перв. примен.	
Инв. № подл.		Инв. № докл.	
Подп. и дата		Подп. и дата	
Взам. инв. №		Инв. № докл.	
Подп. и дата		Подп. и дата	
Инв. № подл.		Инв. № докл.	

ТФРП.401.362281.01.00141 Q

Technical drawing of a part with dimensions and annotations. The drawing shows a side view of a component with a total length of 1803,4 and a width of 400. The left end has a semi-circular profile with a radius of 10 mm. The right end has a rectangular profile with a width of 400. The drawing includes several cross-sectional views with dimensions: 2°1', 0°49', 0°32', 0°21', 0°14', 0°9', 0°5', 0°2', 0°1', 0°38', and 0°33'. The drawing also includes the text 'Гравировка гудов' and 'Гравировка'.

1 Неуказанный внутренний радиус гуда 10 мм

2 Гнуть по гравировке. Гравировка снаружи

3 Проверить по кондуктору ТФРП.401.362281.01.00141-02


ТФРП.401.362281.01.00141			
Стенка 1		Лист	Масса
		1	11,9
		Листов	2
Сталь 10 ГОСТ 1050-2013			

Копировал
Формат А4


ТФРП.401.362281.01.00141

ТФРП.401.362281.01.00141 -01 – зеркальное отражение

Остальное – см. ТФРП.401.362281.01.00141 Q

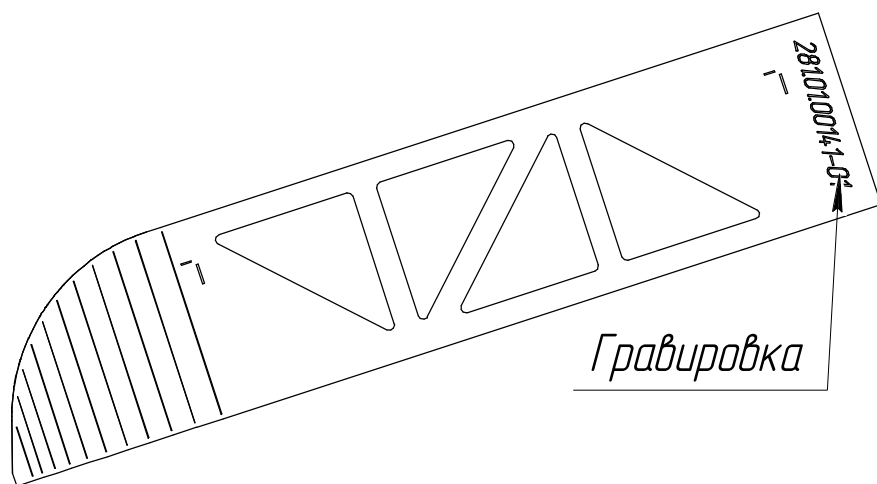

ТФРП.401.362281.01.00141-02 Кондуктор(1:5) Q

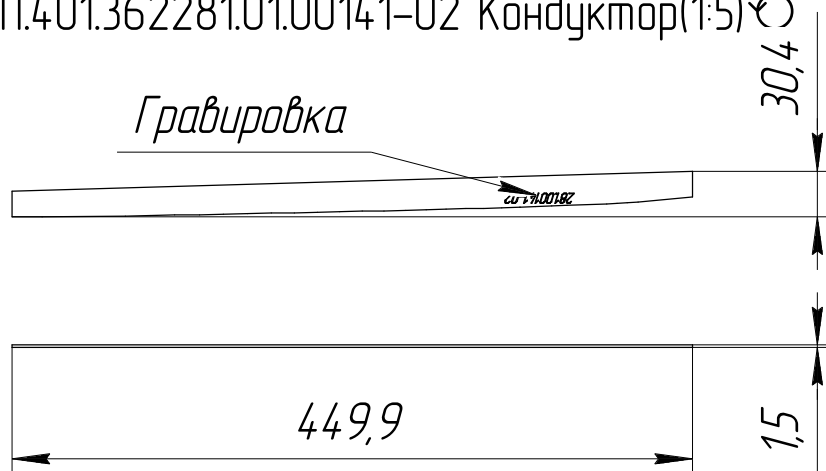


Инв. № подл.	Подп. и дата	Взам. инв. №	Инв. № дубл.	Подп. и дата
Изм.	Лист	№ докум.	Подп.	Дата
ТФРП.401.362281.01.00141				
Копировал				
Формат А4				
Лист				2

Инв. № подл.		Подп. и дата		Взам. инв. №		Инв. № дубл.		Подп. и дата		Справ. №		Перв. примен.	
<div style="display: flex; justify-content: space-between;"> <div> <p>ТФРП.401.362281.01.00142</p> <p>Стенка 2</p> <p>Сталь 10 ГОСТ 1050-2013</p> </div> <div> <p>1 Неуказанный внутренний радиус гиба 10 мм</p> <p>2 Гнуть по гравировке. Гравировка снаружи</p> <p>3 Проверить по кондуктору ТФРП.401.362281.01.00142-02</p> </div> </div>													
Изм. Лист		№ докум.		Подп.		Дата		<div style="display: flex; justify-content: space-between;"> <div> <p>ТФРП.401.362281.01.00142</p> <p>Стенка 2</p> <p>Сталь 10 ГОСТ 1050-2013</p> </div> <div> <p>1 Неуказанный внутренний радиус гиба 10 мм</p> <p>2 Гнуть по гравировке. Гравировка снаружи</p> <p>3 Проверить по кондуктору ТФРП.401.362281.01.00142-02</p> </div> </div>					
Разраб.		Ахметова											
Пров.													
Т.контр.													
Н.контр.								<div style="display: flex; justify-content: space-between;"> <div> <p>ТФРП.401.362281.01.00142</p> <p>Стенка 2</p> <p>Сталь 10 ГОСТ 1050-2013</p> </div> <div> <p>1 Неуказанный внутренний радиус гиба 10 мм</p> <p>2 Гнуть по гравировке. Гравировка снаружи</p> <p>3 Проверить по кондуктору ТФРП.401.362281.01.00142-02</p> </div> </div>					
Утв.													

ТФРП.401.362281.01.00142


ТФРП.401.362281.01.00142 Q

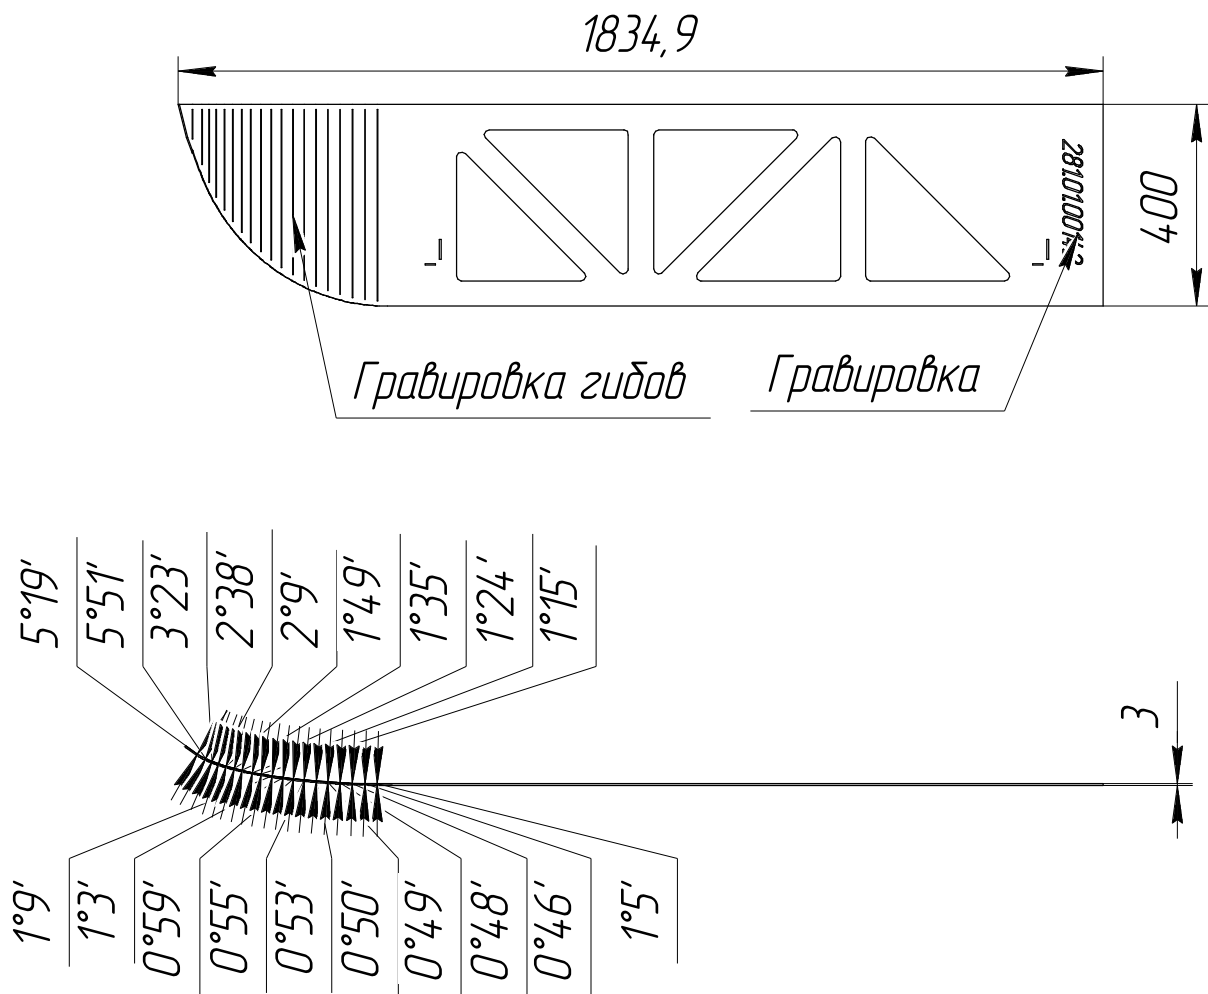

ТФРП.401.362281.01.00142


ТФРП.401.362281.01.00142 -01 – зеркальное отражение

Остальное – см. ТФРП.401.362281.01.00142 Q

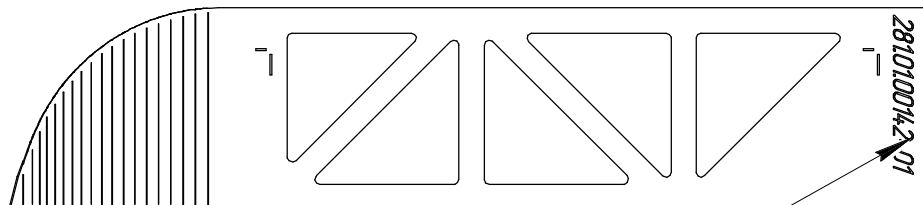

Гравировка

ТФРП.401.362281.01.00142-02 Кондуктор

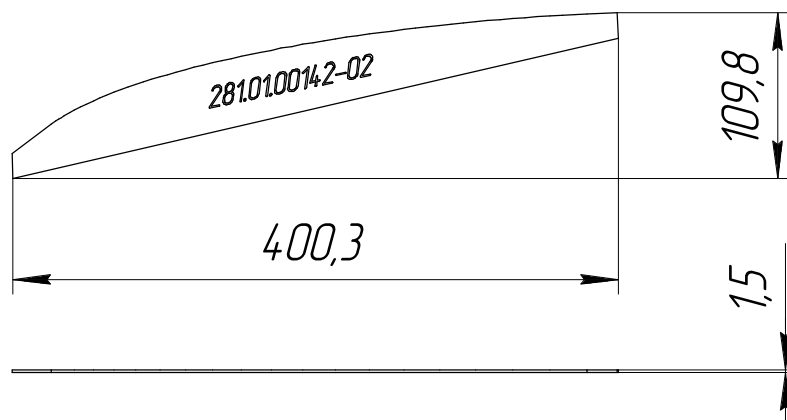

Инв. № подл.	Подп. и дата	Взам. инв. №	Инв. № дубл.	Подп. и дата
Изм.	Лист	№ докум.	Подп.	Дата
ТФРП.401.362281.01.00142				
Копировал				Лист
Формат А4				2

Перв. примен.		Справ. №		<div>ТФРП.401.362281.01.00143</div>	
				<div>ТФРП.401.362281.01.00143</div> <div>Гравировка</div> <div> <div>400</div> <div>2810100143</div> <div>1880,6</div> <div>3</div> </div>	
				<div>ТФРП.401.362281.01.00143 -01 – зеркальное отражение</div> <div>Остальное – см. ТФРП.401.362281.01.00143</div> <div> <div>2810100143-01</div> <div>Гравировка</div> </div>	
Подп. и дата		Взам. инв. №		Инв. № дубл.	
Подп. и дата					
Инв. № подл.					
Изм. Лист		№ докум.		Подп.	
Разраб.		Ахметова			
Пров.					
Т.контр.					
Н.контр.					
Утв.					
<div>ТФРП.401.362281.01.00143</div> <div>Стенка 3</div> <div>Сталь 10 ГОСТ 1050-2013</div>				<div>Лист</div> <div>Масса</div> <div>Масштаб</div> <div>9,29</div> <div>1:15</div> <div>Лист</div> <div>Листов</div> <div>1</div>	
Копировал				Формат А4	

Перв. примен.		Справ. №		Инв. № докл.		Взам. инв. №		Подп. и дата		Инв. № подл.			
<div style="text-align: right;">ТФРП.401.362281.01.00144</div> <div style="text-align: center;"> <p>ТФРП.401.362281.01.00144 Q</p> </div> <div style="margin-top: 10px;"> <p>1 Неуказанный внутренний радиус гуда 10 мм</p> <p>2 Проверить по кондуктору ТФРП.401.362281.01.0144-02</p> </div>													
Подп. и дата		Подп. и дата		Подп. и дата		Подп. и дата		ТФРП.401.362281.01.00144					
Изм. Лист		№ докум.		Подп.		Дата		Обечайка верхняя		Лист	Масса	Масштаб	
Разраб.		Ахметова									5,25	1:20	
Пров.										Лист	1	Листов	2
Т.контр.													
Н.контр.								Сталь 10 ГОСТ 1050-2013					
Утв.													




ТФРП.401.362281.01.00144

ТФРП.401.362281.01.00144 -01 – зеркальное отражение

Остальное – см. ТФРП.401.362281.01.00144 Q



ТФРП.401.362281.01.00144-02 Кондуктор

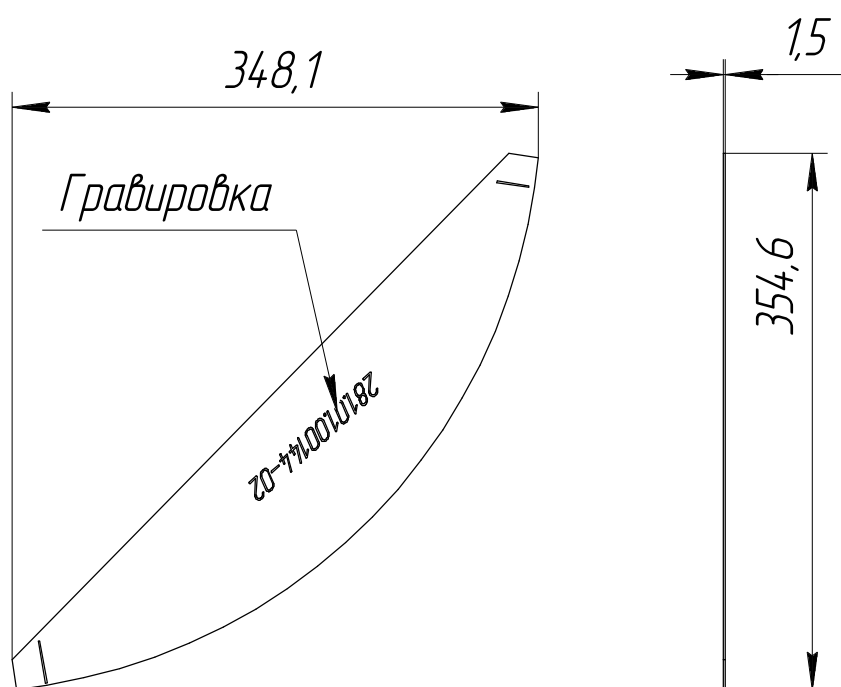


Инв. № подл.	Подп. и дата	Взам. инв. №	Инв. № доп.	Подп. и дата
Изм.	Лист	№ докум.	Подп.	Дата
ТФРП.401.362281.01.00144				
Копировал				
Формат А4				
				Лист
				2

Справ. №		Перв. примен.	
<div style="text-align: right;">ТФРП.401.362281.01.00144.01Q</div> <div style="text-align: center;"> </div>			
Инв. № подл.	Т.контр.	Н.контр.	Утв.
Изм. Лист	№ докум.	Подп.	Дата
Разраб.	Ахметова		
Пров.			
<div style="text-align: center;">ТФРП.401.362281.01.00144.01</div> <div style="text-align: center;">Обечайка верхняя</div> <div style="text-align: center;">Сталь 10 ГОСТ 1050-2013</div>			
Лист 1		Листов 2	
Масса 5,27		Масштаб 1:15	

ТФРП.401.362281.01.00144.01

ТФРП.401.362281.01.00144.01 – зеркальное отражение

Остальное – см. ТФРП.401.362281.01.00144.01

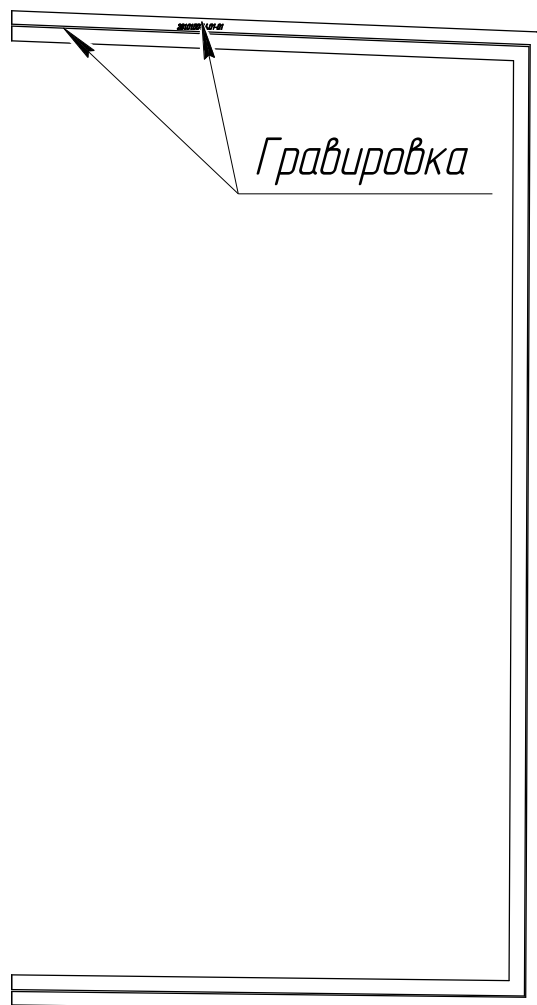

Инв. № подл.	Подп. и дата	Взам. инв. №	Инв. № дубл.	Подп. и дата
Изм.	Лист	№ докум.	Подп.	Дата
ТФРП.401.362281.01.00144.01				
Копировал				Лист
Формат А4				2

Инв. № подл.


Инв. № подл.

Формат А4

1001013622810100145

ТФРП.401.362281.01.00145-01 – зеркальное отражение


Остальное – см. ТФРП.401.362281.01.00145

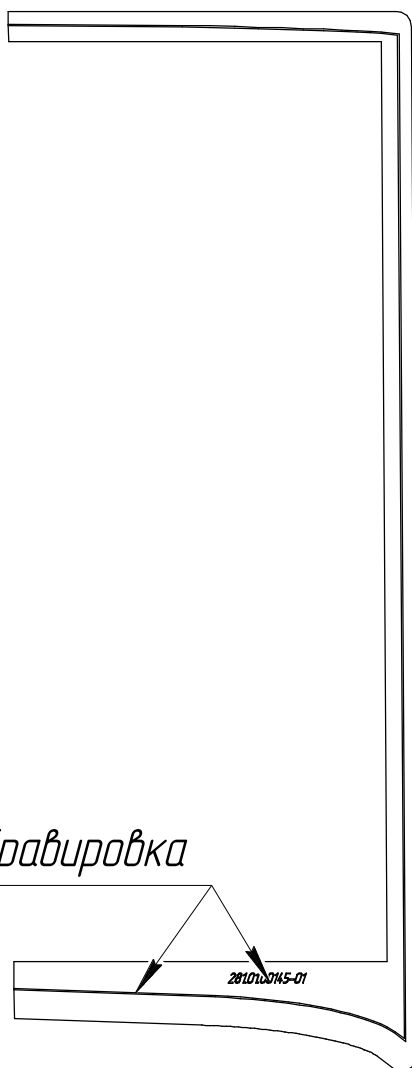

Гравировка

28101-0145-01

Инв. № подл.	Подп. и дата	Взам. инв. №	Инв. № дубл.	Подп. и дата

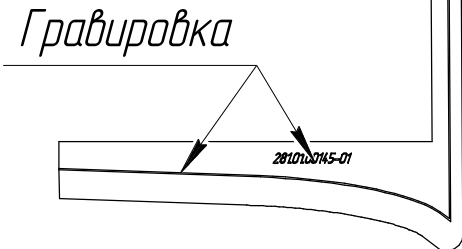

Гравировка

28101.00145-01


					ТФРП.401.362281.01.00145	Лист
Изм.	Лист	№ докум.	Подп.	Дата		2

Перв. примен.		Справ. №		Подп. и дата		Взам. инв. №		Инв. № дубл.		Подп. и дата		Инв. № подл.																																			
<div>ТФРП.401.362281.01.00145.01</div> <div><div>1997,7</div><div>1061,1</div><div>3</div><div>Гравировка</div></div>												ТФРП.401.362281.01.00145.01																																			
<table><tr><td colspan="5">ТФРП.401.362281.01.00145.01</td><td colspan="3">Лист</td><td colspan="2">Масса</td><td colspan="2">Масштаб</td></tr><tr><td colspan="5">Фланец</td><td colspan="3"></td><td colspan="2">6,45</td><td colspan="2">1:15</td></tr><tr><td colspan="5">Сталь 10 ГОСТ 1050-2013</td><td colspan="3">Лист 1</td><td colspan="2">Листов 2</td><td colspan="2"></td></tr></table>												ТФРП.401.362281.01.00145.01					Лист			Масса		Масштаб		Фланец								6,45		1:15		Сталь 10 ГОСТ 1050-2013					Лист 1			Листов 2			
ТФРП.401.362281.01.00145.01					Лист			Масса		Масштаб																																					
Фланец								6,45		1:15																																					
Сталь 10 ГОСТ 1050-2013					Лист 1			Листов 2																																							
Изм. Лист					№ докум.					Подп.		Дата																																			
Разраб.					Ахметова	
Пров.	
Т.контр.	
Н.контр.	
Утв.	



ТФРП.401.362281.01.00145.01

ТФРП.401.362281.01.00145.01-01 – зеркальное отражение

Остальное – см. ТФРП.401.362281.01.00145.01

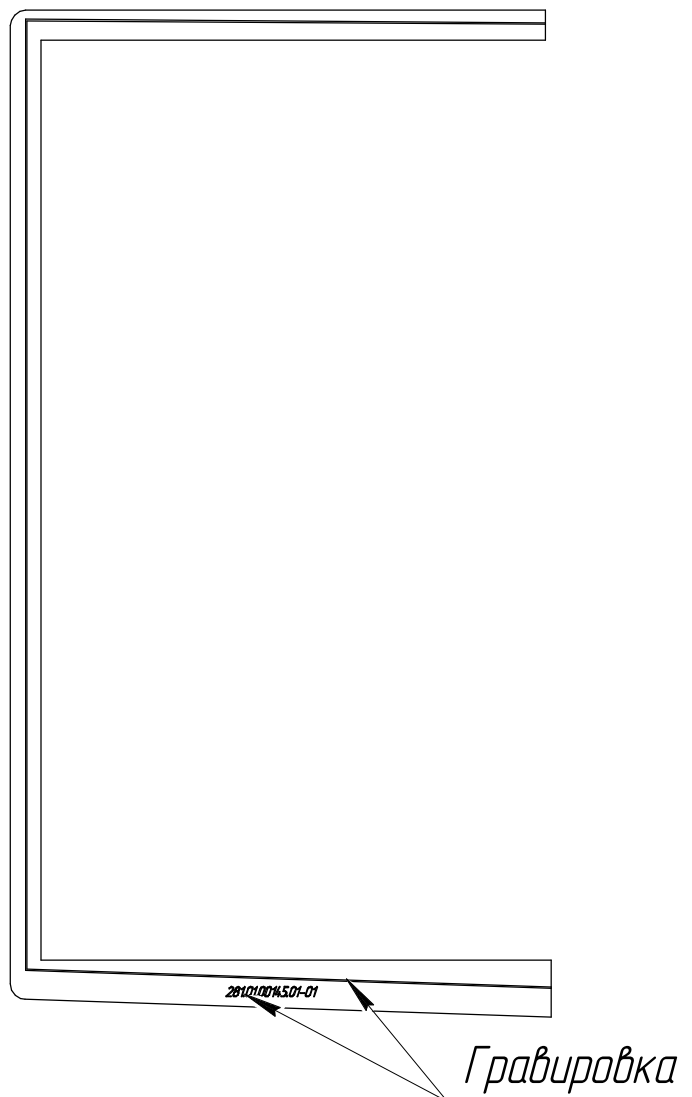

Инв. № подл.	Подп. и дата	Взам. инв. №	Инв. № дубл.	Подп. и дата
Изм.	Лист	№ докум.	Подп.	Дата
ТФРП.401.362281.01.00145.01				
Копировал				
Формат А4				
				Лист
				2

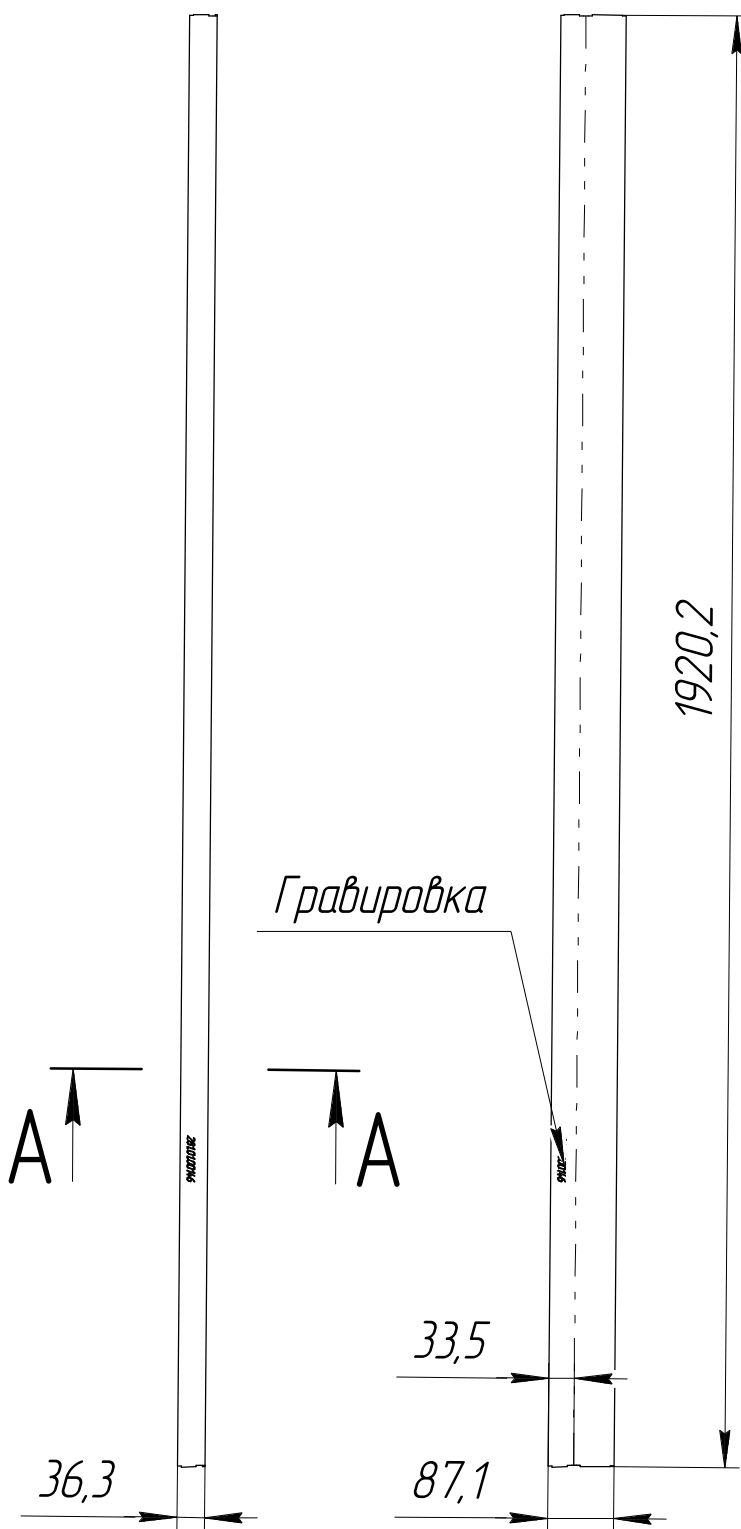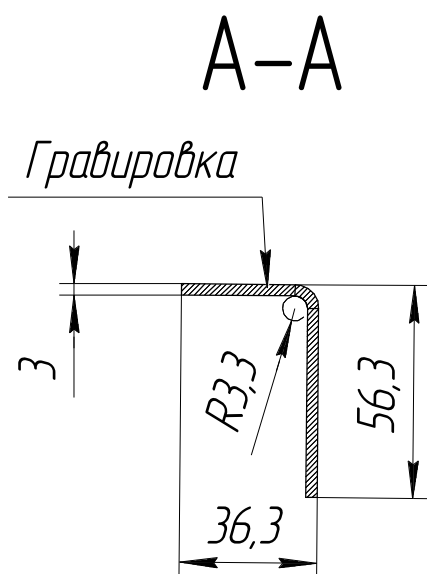

					ТФРП.401.362281.01.00146				
					Уголок	Лит.		Масса	Масштаб
Изм.	Лист	№ докум.	Подп.	Дата				3,96	1:10
Разраб.	Ахметова								
Пров.									
Т.контр.						Лист	1	Листов	2
					Сталь 10 ГОСТ 1050-2013				
Н.контр.									
Утв.									




ТФРП.401.362281.01.00146

ТФРП.401.362281.01.00146-02 – зеркальное отражение

Остальное – см. ТФРП.401.362281.01.00146Q

Гравировка

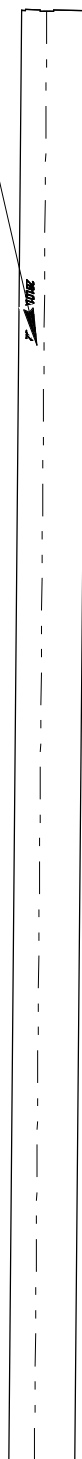

Инв. № подл.	Подп. и дата	Взам. инв. №	Инв. № дубл.	Подп. и дата
Изм.	Лист	№ докум.	Подп.	Дата
ТФРП.401.362281.01.00146				
Копировал				
Формат А4				
				Лист
				2


Формат А4

ТФРП.401.362281.01.00146 -01

ТФРП.401.362281.01.00146 -03 – зеркальное отражение

Остальное – см. ТФРП.401.362281.01.00146 -01Q,

Гравировка

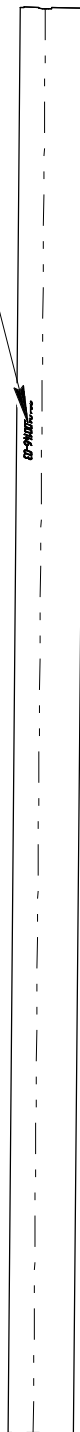

Инв. № подл.	Подп. и дата	Взам. инв. №	Инв. № дубл.	Подп. и дата
Изм.	Лист	№ докум.	Подп.	Дата
ТФРП.401.362281.01.00146 -01				
Копировал				Лист
Формат А4				2