

93 0010001018229510711dф1

ТФРП.401.362281.01.00100

Выполнить сборку в следующем порядке:
1. Варить ТФРП.401.362281.01.00101 к ТФРП.401.362281.01.00101.01 и ТФРП.401.362281.01.00105 к ТФРП.401.362281.01.00105.01 стыковым швом С7
2. Варить ТФРП.401.362281.01.00106 и ТФРП.401.362281.01.00106-01 к ТФРП.401.362281.01.00102 внутри швом Т1, снаружи варить через пазы.
3. Приварить ТФРП.401.362281.01.00103, ТФРП.401.362281.01.00104 угловым швом У4
4. Установить по гравировке на ТФРП.401.362281.01.00105 и ТФРП.401.362281.01.00105.01. Варить шахматным швом ТЗ
5. Приварить ТФРП.401.362281.01.00101 и ТФРП.401.362281.01.00101.01 гравировкой вверх шахматным швом ТЗ

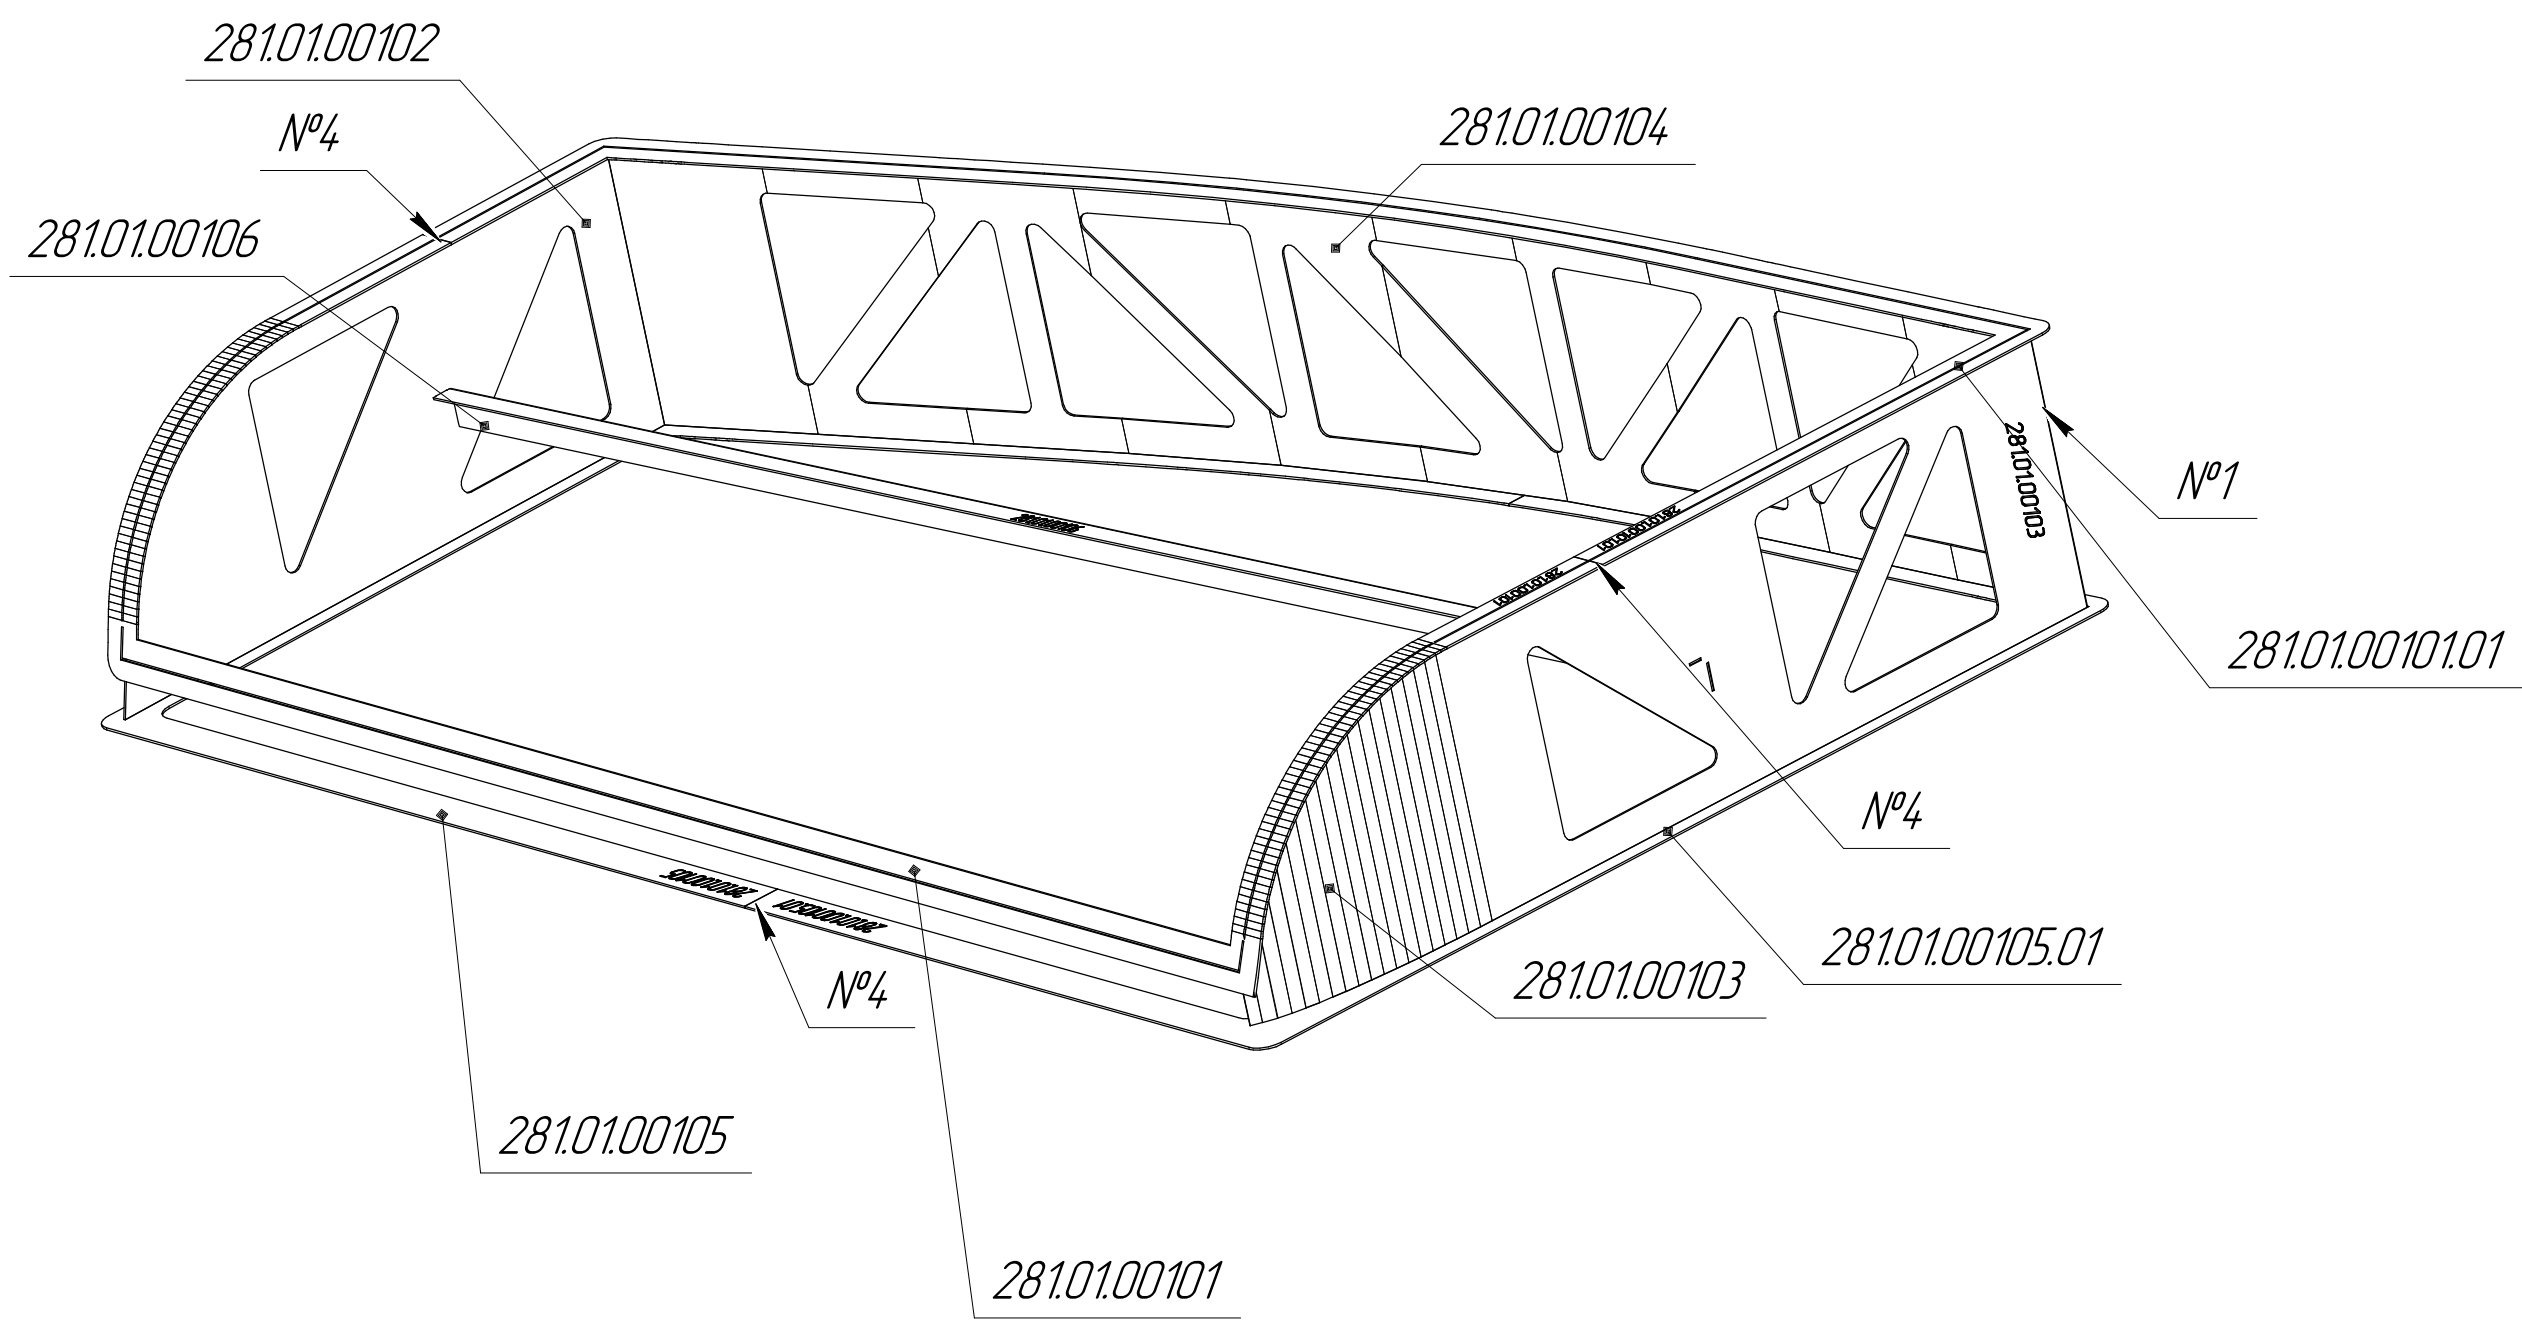


Таблица сварных швов

				S	S1	b		e	e1	g	K	
						Номин.	Пред откл					
№1	У4			3	3	0	+1			1±0.5		ГОСТ 14 771-76
№2	ТЗ- K-50z100			3	3						4+3	ГОСТ 14 771-76
№3	Т1			3	3						4+3	ГОСТ 14 771-76
№4	С7			3	4						4+3	ГОСТ 14 771-76

Формат	Зона	Паз	Обозначение	Наименование	Кол	Примечание
			Переменные данные для исполнений:			
				ТФРП.401.362281.01.00100		
			Детали			
*)	1	ТФРП.401.362281.01.00101	Верхняя обечайка		1	*12хА4
			Верхняя обечайка		1	
А4	3	ТФРП.401.362281.01.00102	Стенка 1		1	
*)	4	ТФРП.401.362281.01.00103	Стенка 2		1	*12хА4
*)	5	ТФРП.401.362281.01.00104	Стенка 3		1	*12хА4
*)	6	ТФРП.401.362281.01.00105	Фланец		1	*12хА4
*)	7	ТФРП.401.362281.01.00105.01	Фланец		1	*12хА4
*)	8	ТФРП.401.362281.01.00106	Уголок		1	*12хА4
			ТФРП.401.362281.01.00100-1			
			Детали			
	1	ТФРП.401.362281.01.00101-01	Верхняя обечайка		1	
	2	ТФРП.401.362281.01.00101.01-01	Верхняя обечайка		1	
А4	3	ТФРП.401.362281.01.00102-01	Стенка 1		1	
	4	ТФРП.401.362281.01.00103-01	Стенка 2		1	
	5	ТФРП.401.362281.01.00104-01	Стенка 3		1	
*)	6	ТФРП.401.362281.01.00105-01	Фланец		1	*12хА4
*)	7	ТФРП.401.362281.01.00105.01-01	Фланец		1	*12хА4
*)	8	ТФРП.401.362281.01.00106-01	Уголок		1	*12хА4
			ТФРП.401.362281.01.00100 СБ			
Изм. Лист	№ докум.	Подп.	Дата	Оснастка стекла 10 Сборочный чертеж		
Разраб.	Ахметова					
Проб.						
Т.контр.						
Н.контр.						
Утв.						
				Лист	Масса	Масштаб
				1	56,18	1:10
				Листов	1	Листов 3
				Копировал		
				Формат А2		

Перв. примен.

Сград. №

Подп. и дата

Инд. № дроб.



Взам. инв. №

Подп. и дата


Инд. № подл.

Выдержать размер по гравировке


Г-Г

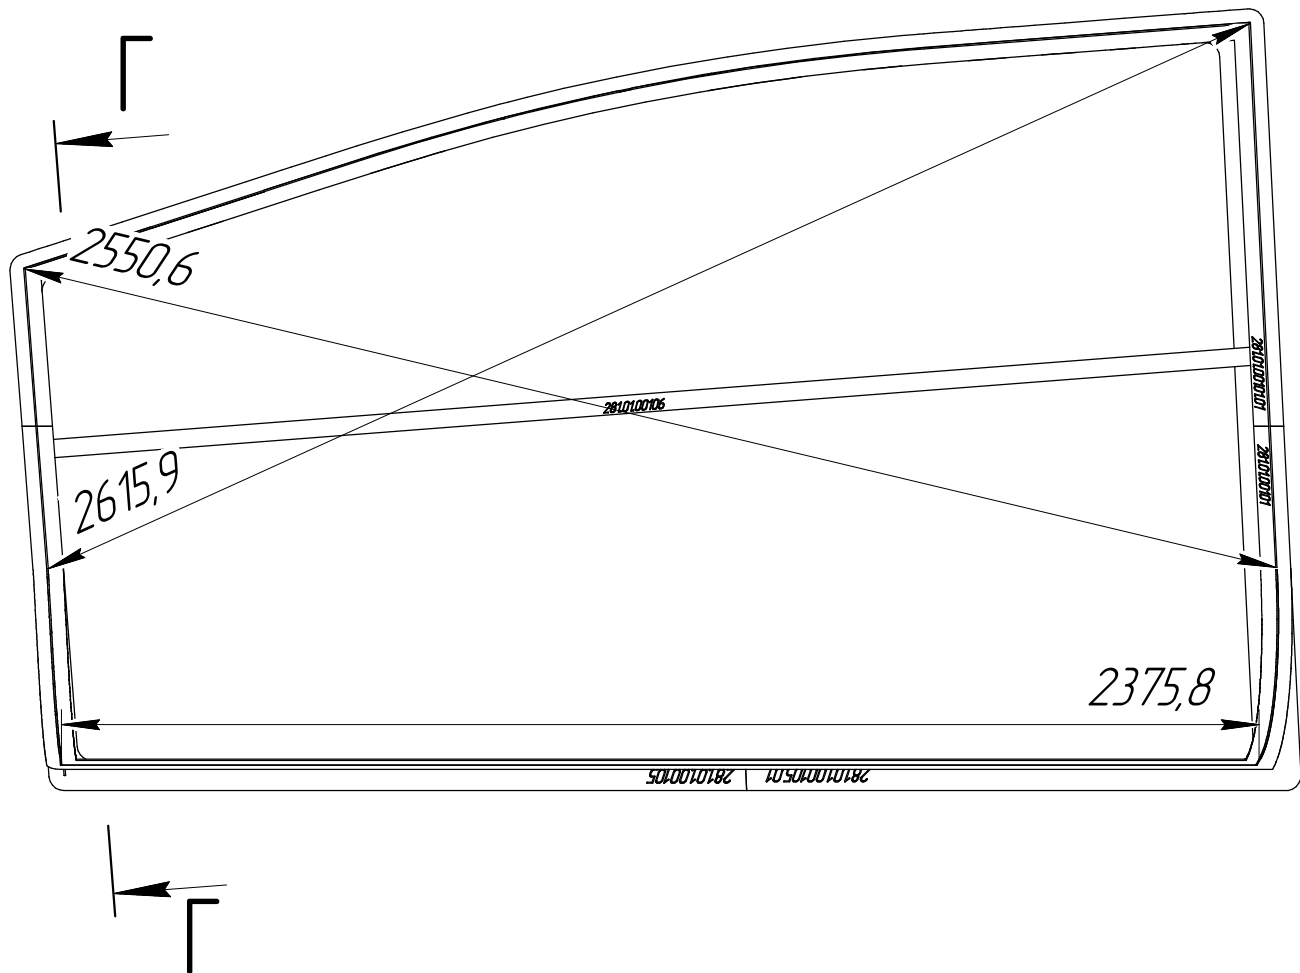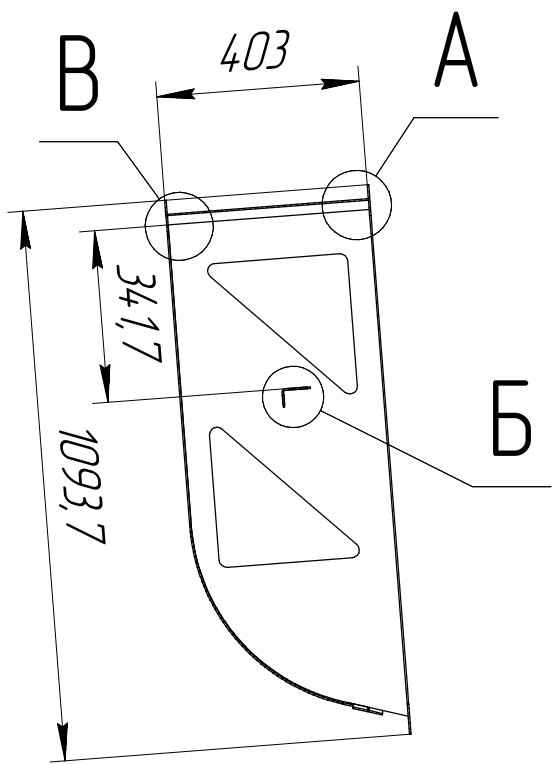


А

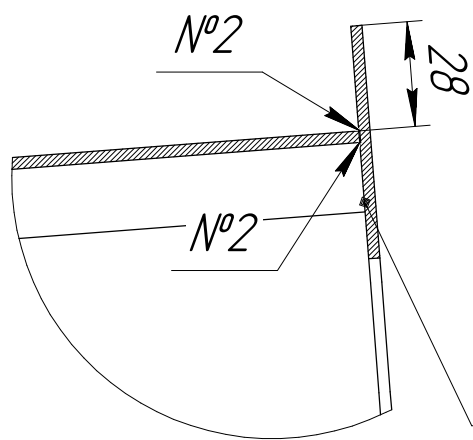

Б

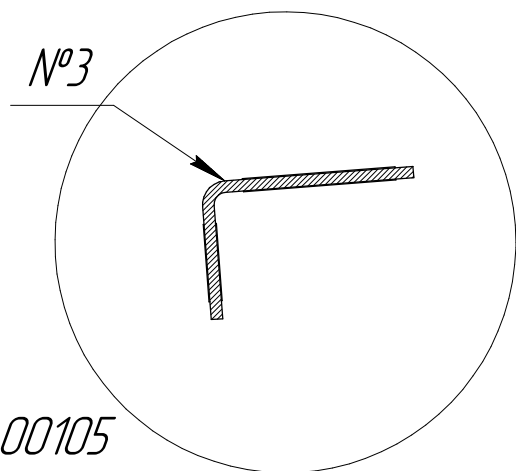

В

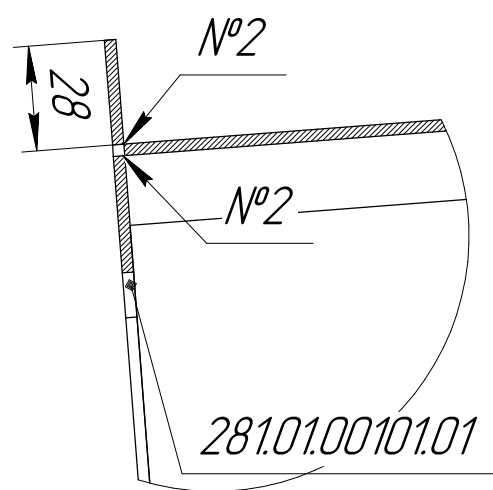

Инв. № подл.	Подп. и дата	Взам. инв. №	Инв. № дубл.	Подп. и дата

Изм.	Лист	№ докум.	Подп.	Дата

ТФРП.401.362281.01.00100 СБ

Копировал

Формат А3

[illegible]

Изм.	Лист	№ докум.	Подп.	Дата

Лист
3