


Перв. примен.		Формат	Зона	Поз.	Обозначение	Наименование	Кол.	Примечание
					Переменные данные для исполнений:			
						ТФРП.401.362281.01.00110		
						Детали		
Справ. №	*	1	ТФРП.401.362281.01.00111	Стенка 1	1	*12хА3		
	*	2	ТФРП.401.362281.01.00112	Стенка 2	1	*12хА4		
		3	ТФРП.401.362281.01.00113	Стенка 3	1			
	*	4	ТФРП.401.362281.01.00114	Обечайка верхняя	1	*12хА4		
	*	5	ТФРП.401.362281.01.00114.01	Обечайка верхняя	1	*12хА4		
	*	6	ТФРП.401.362281.01.00115	Уголок	1	*12хА4		
	*	7	ТФРП.401.362281.01.00115-01	Уголок	1	*12хА4		
	*	8	ТФРП.401.362281.01.00116	Фланец	1	*12хА4		
	*	9	ТФРП.401.362281.01.00116.01	Фланец	1	*12хА4		
						ТФРП.401.362281.01.00110-1		
						Детали		
Взам. инв. №	*	4	ТФРП.401.362281.01.00114-01	Обечайка верхняя	1	*12хА4		
	*	5	ТФРП.401.362281.01.00114.01-01	Обечайка верхняя	1	*12хА4		
	*	6	ТФРП.401.362281.01.00115-02	Уголок	1	*12хА4		
	*	8	ТФРП.401.362281.01.00116-01	Фланец	1	*12хА4		
Подп. и дата	*	9	ТФРП.401.362281.01.00116.01-01	Фланец	2	*12хА4		
		10	ТФРП.401.362281.01.00111 -01	Стенка 1	1			
					ТФРП.401.362281.01.00110			
Инв. № подл.	Изм.	Лист	№ докум.	Подп.	Дата	Оснастка стекла 11		
	Разраб.							
	Пров.							
	Н.контр.							
	Утв.					Лит.	Лист	Листов
							1	2

[illegible]




ТФРП.401.36228101.00111

ТФРП.401.36228101.00111 –01 – зеркальное отражение  
Остальное – см. ТФРП.401.36228101.00111 О<sub>3</sub>

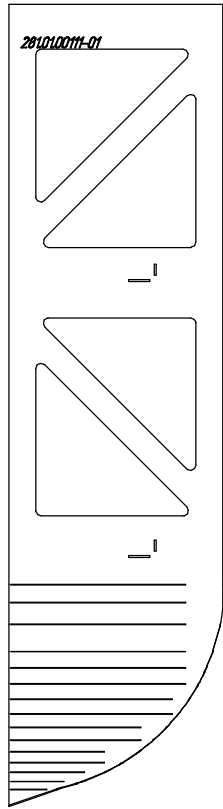

ТФРП.401.36228101.00111 –02 Кондуктор

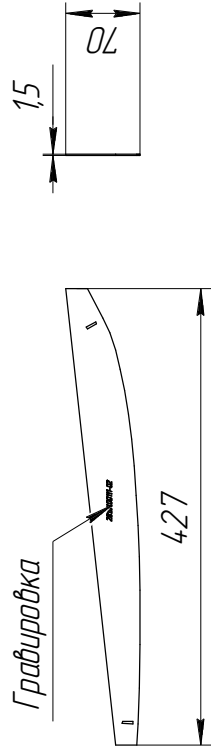

ИИВ, № подл.	Подп. и дата	Взам. ИИВ, №	ИИВ, № дубл.	Подп. и дата
--------------	--------------	--------------	--------------	--------------

Изм./лист	№ докум.	Подп.	Дата	ТФРП.401.36228101.00111	Лист
					2
Копировал					А3
Формат					

Справ. №		Перв. примен.	
Инв. № подл.		Подп. и дата	
Т.контр.		Инв. № докл.	
Н.контр.		Взам. инв. №	
Утв.		Подп. и дата	

ТФРП.401.362281.01.00112 Q

Гравировка гйда

Гравировка

1625

400

3

0°14' 3°40' 2°2' 1°15' 1°7' 0°47' 0°21' 0°16' 0°9' 0°11' 0°4' 0°4' 0°2' 0°2' 0°7' 0°51'

1 Внутренний радиус гйда 10 мм  
2 Гнуть по гравировке. Гравировка снаружи  
3 Проверить по кондуктору ТФРП.401.362281.00112-02

ТФРП.401.362281.01.00112			
Изм. Лист Разраб. Пров. Т.контр.	№ докум. Мантров	Подп.	Дата
Стенка 2			
Сталь 10 ГОСТ 1050-2013			

Лит.	Масса	Масштаб
10,22	1:10	
Лист 1	Листов 2	


Копировал

Формат А4


ТФРП.401.362281.01.00112

ТФРП.401.362281.01.00112 -01 – зеркальное отражение

Остальное – см. ТФРП.401.362281.01.00112 Q

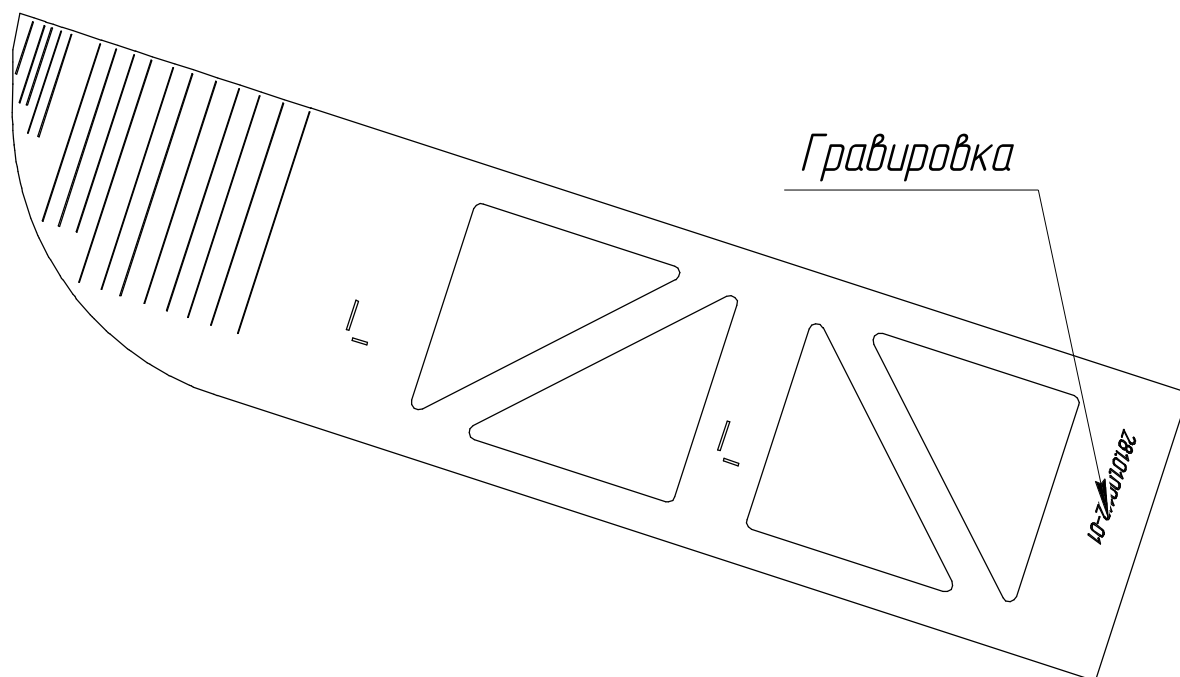

ТФРП.401.362281.01.00112-02 Кондуктор(1:5) Q

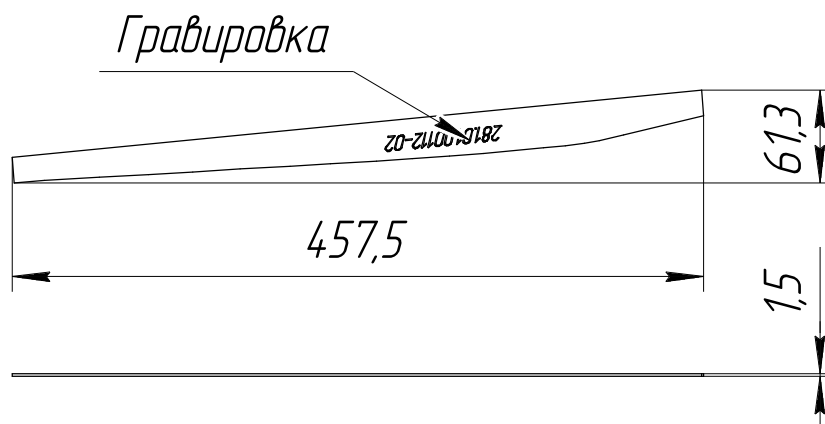



Инв. № подл.	Подп. и дата	Взам. инв. №	Инв. № докл.	Подп. и дата
Изм.	Лист	№ докум.	Подп.	Дата
ТФРП.401.362281.01.00112				
Копировал				Лист
Формат А4				2

Справ. №		Перв. примен.		ТФРП.401.362281.01.00113					
Подп. и дата		Взам. инв. №		Инв. № дубл.		Подп. и дата		<div><div><div>1849</div><div>400</div></div><div><div>Гравировка</div><div>2810100113</div></div><div>3</div></div>	
Изм. Лист		№ докум.		Подп.		Дата			
Разраб.		Мантров							
Пров.									
Т.контр.									
Ив. № подл.		Н.контр.		Утв.		Сталь 10 ГОСТ 1050-2013		Лист 1 Листов 2	
						Стенка 3		Масса 9 Масштаб 1:10	
						ТФРП.401.362281.01.00113			

ТФРП.401.362281.01.00113 -01 – зеркальное отражение



Остальное – см. ТФРП.401.362281.01.00113 ☺

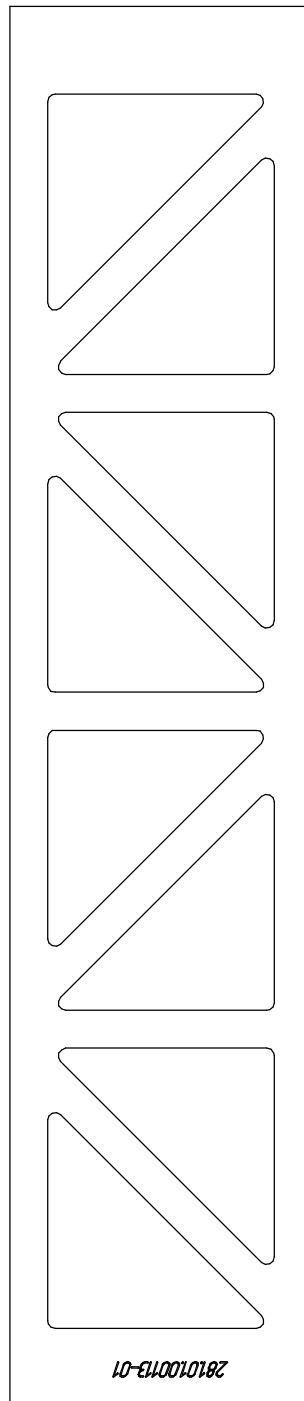

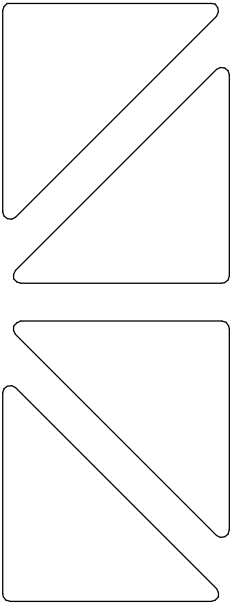Инв. № подл.	Подп. и дата	Взам. инв. №	Инв. № дудл.	Подп. и дата	<div style="border: 1px solid black; padding: 10px; text-align: center;">  <p>2810100113-01</p> </div>
Изм.	Лист	№ докум.	Подп.	Дата	<div style="display: flex; justify-content: space-between; align-items: center;"> <div style="font-size: 2em; font-weight: bold;">ТФРП.401.362281.01.00113</div> <div style="text-align: right;"> <div>Лист</div> <div>2</div> </div> </div>



ТФРП.401.362281.01.00114Q<sub>3</sub>

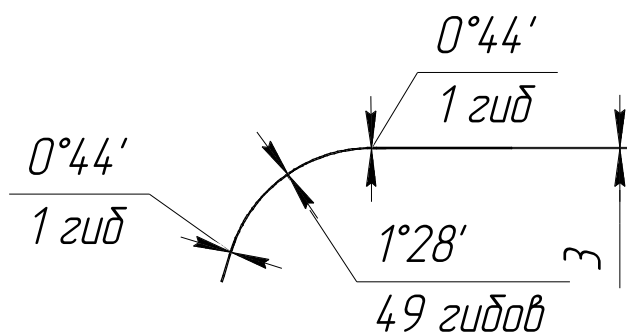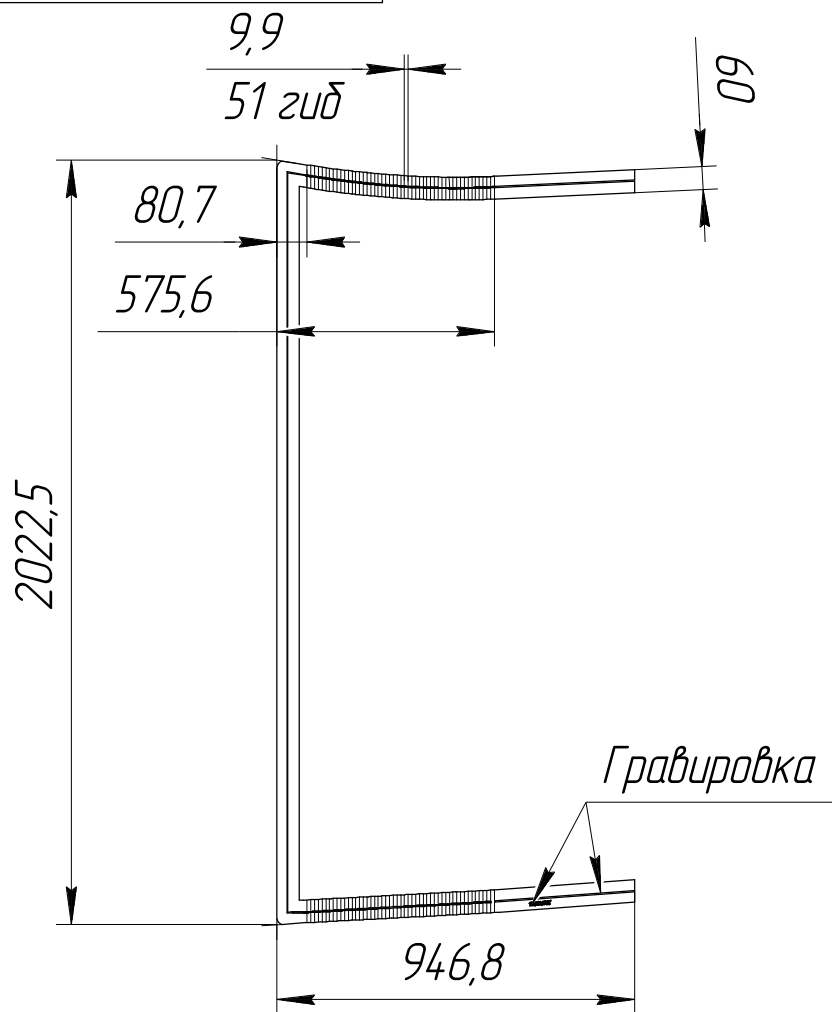

1 Неуказанный внутренний радиус гйда 10 мм  
2 Проверить по гравировке ТФРП.401.362281.01.00114-02

ТФРП.401.362281.01.00114

Обечайка верхняя

Сталь 10 ГОСТ 1050-2013

Лит.	Масса	Масштаб
------	-------	---------

5,1	1:20
-----	------

Лист	1	Листов	2
------	---	--------	---

Копировал

Формат А4


ТФРП.401.362281.01.00114

ТФРП.401.362281.01.00114-01 – зеркальное отражение

Остальное – см. ТФРП.401.362281.01.00114Q



ТФРП.401.362281.01.00114-02 Кондуктор(1:5)

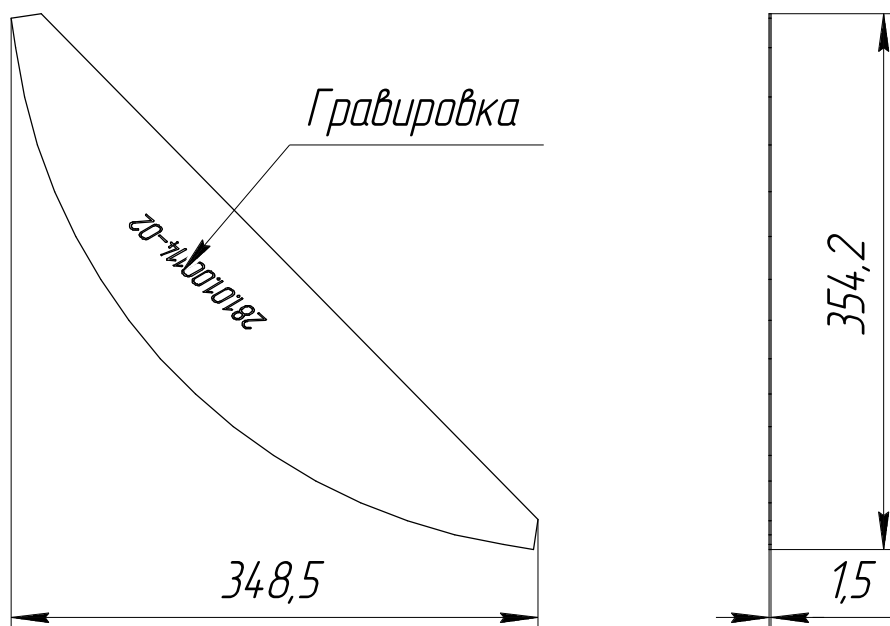

Инв. № подл.	Подп. и дата	Взам. инв. №	Инв. № дубл.	Подп. и дата
Изм.	Лист	№ докум.	Подп.	Дата
ТФРП.401.362281.01.00114				Лист
				2

Копировал


Формат А4

ноб 2


ТФРП.401.362281.01.00114.01

ТФРП.401.362281.01.00114.01-01 – зеркальное отражение

Остальное – см. ТФРП.401.362281.01.00114.01

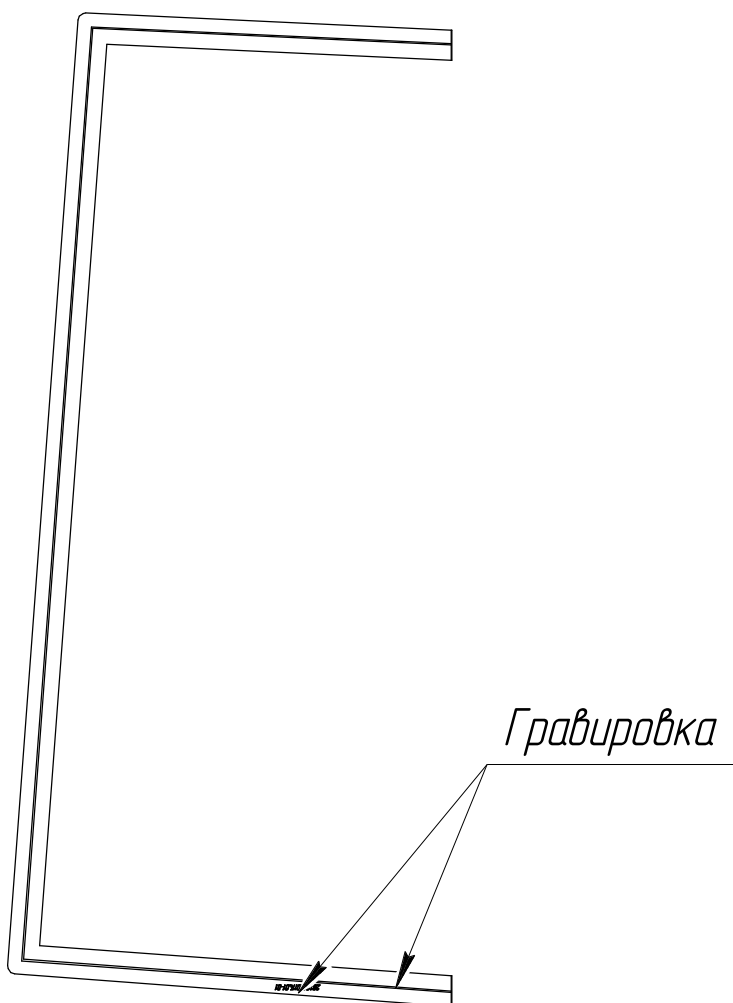


Инв. № подл.	Подп. и дата	Взам. инв. №	Инв. № дубл.	Подп. и дата
Изм.	Лист	№ докум.	Подп.	Дата
ТФРП.401.362281.01.00114.01				
Копировал				Лист
Формат А4				2

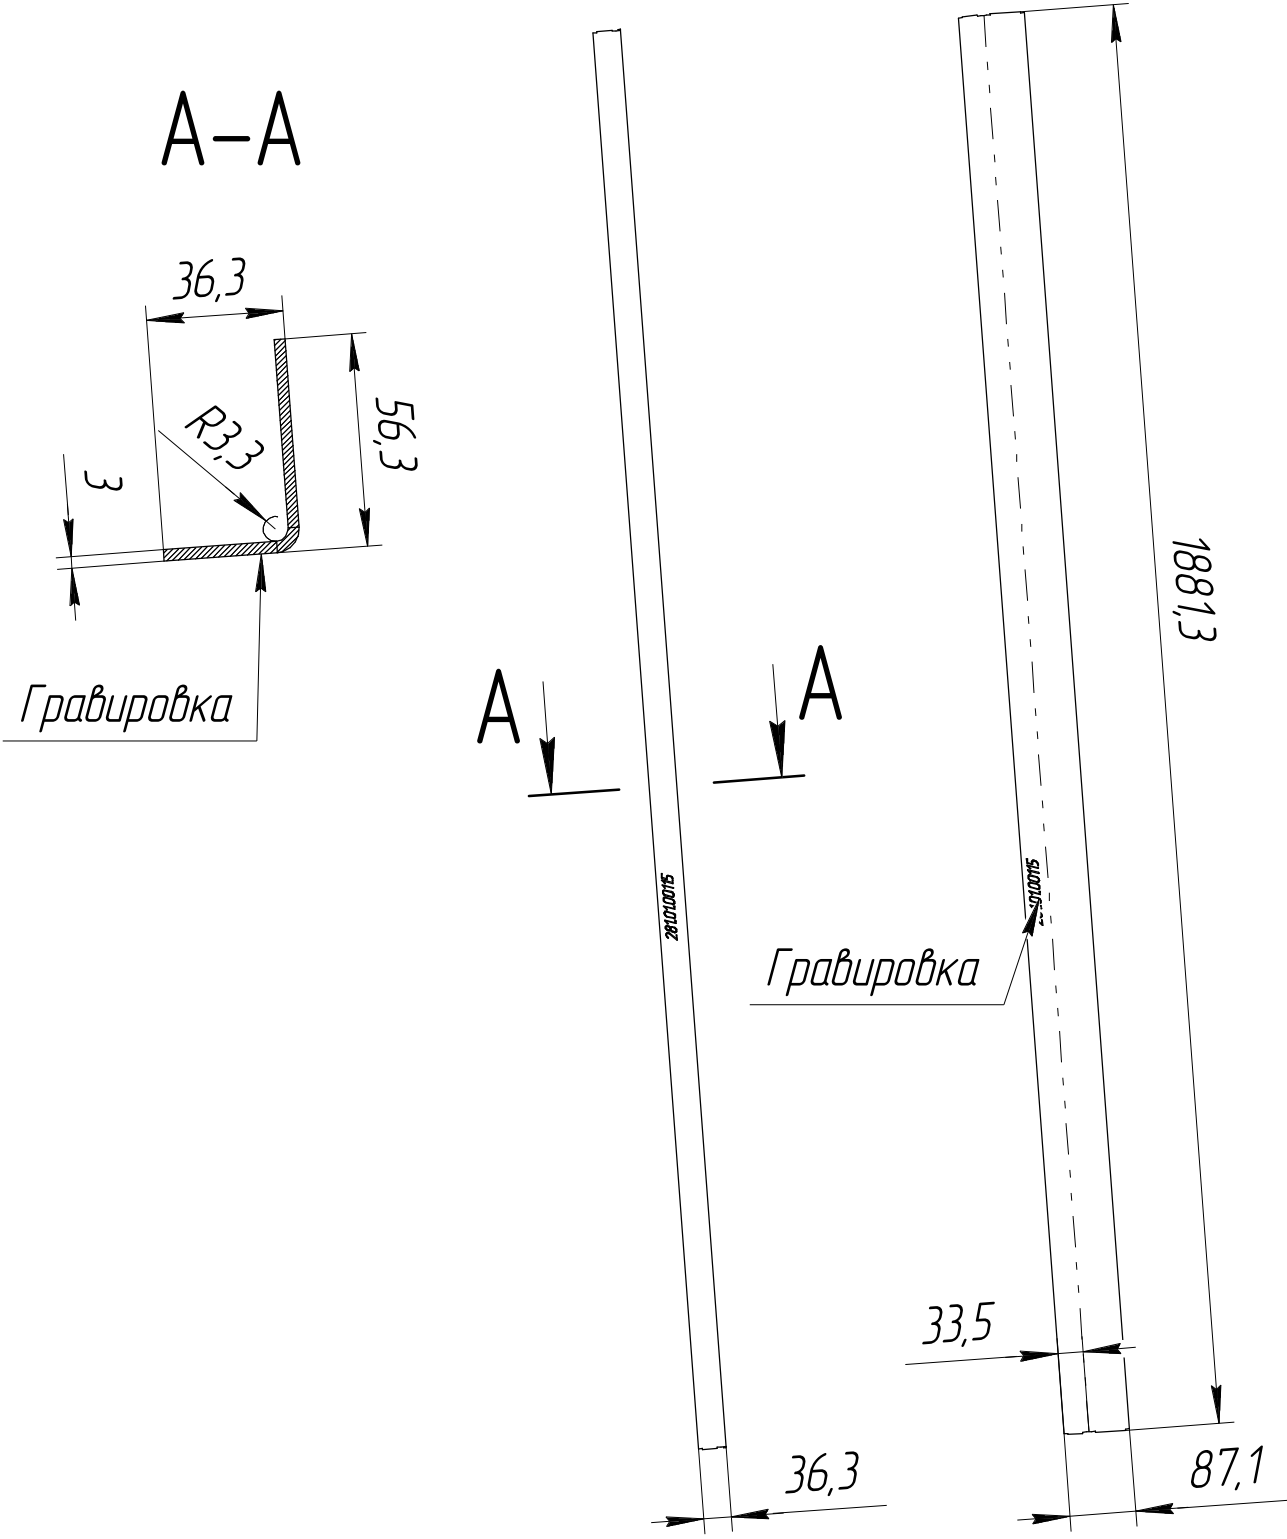Справ. №		Перв. примен.		ТФРП.401.362281.01.00115													
Инв. № подл.		Подп. и дата		ТФРП.401.362281.01.00115Q													
Т.контр.		Инв. № докл.															
Пров.		Взам. инв. №		ТФРП.401.362281.01.00115													
Разраб.		Подп. и дата		Уголок													
Изм. Лист		Инв. № докл.		<table border="1"> <tr> <td>Лист</td> <td>1</td> <td>Масса</td> <td>3,88</td> <td>Масштаб</td> <td>1:10</td> </tr> <tr> <td>Листов</td> <td>2</td> <td colspan="4"></td> </tr> </table>		Лист	1	Масса	3,88	Масштаб	1:10	Листов	2				
Лист	1	Масса	3,88	Масштаб	1:10												
Листов	2																
Н.контр.		Взам. инв. №		Сталь 10 ГОСТ 1050-2013													
Утв.		Подп. и дата		Копировал													
		Инв. № докл.		Формат A4													

ТФРП.401.362281.01.00115

ТФРП.401.362281.01.00115-02 – зеркальное отражение

Остальное – см. ТФРП.401.362281.01.00115Q,

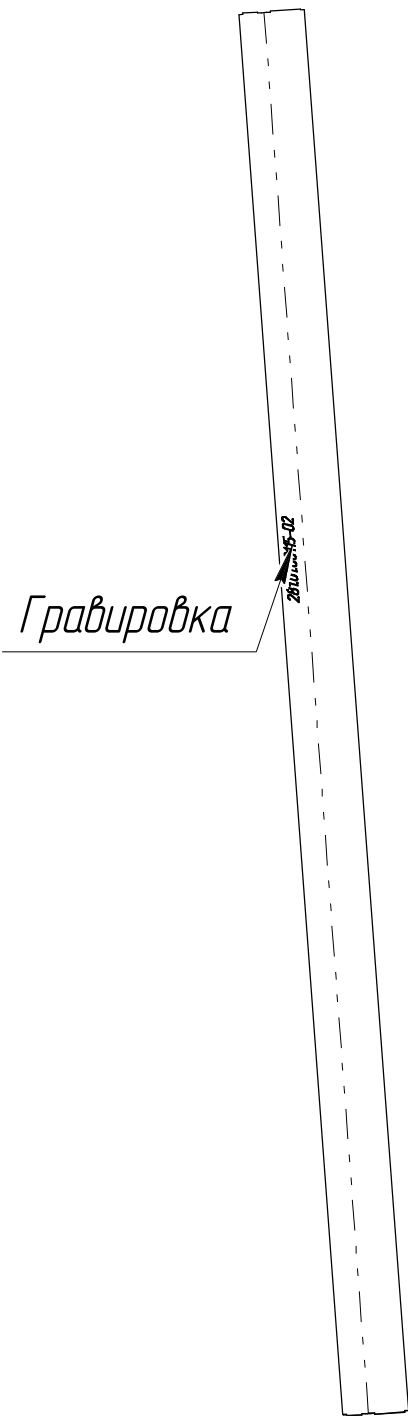

Инв. № подл.	Подп. и дата	Взам. инв. №	Инв. № дубл.	Подп. и дата

Изм.	Лист	№ докум.	Подп.	Дата

ТФРП.401.362281.01.00115				
--------------------------	--	--	--	--


Лист
2

Перв. примен.		Справ. №		Инв. № докл.		Взам. инв. №		Подп. и дата		Инв. № подл.																																				
<div style="display: flex; justify-content: space-between;"> <div> <p>ТФРП.401.362281.01.00115-01</p> <p>ТФРП.401.362281.01.00115-01Q</p> </div> <div> </div> </div>	
<table border="1" style="width: 100%;"> <tr> <td colspan="4"></td> <td colspan="4">ТФРП.401.362281.01.00115-01</td> </tr> <tr> <td colspan="4"></td> <td colspan="4">Уголок</td> </tr> <tr> <td colspan="4"></td> <td colspan="4">Сталь 10 ГОСТ 1050-2013</td> </tr> </table>																ТФРП.401.362281.01.00115-01								Уголок								Сталь 10 ГОСТ 1050-2013														
				ТФРП.401.362281.01.00115-01	
				Уголок	
				Сталь 10 ГОСТ 1050-2013	
<table border="1" style="width: 100%;"> <tr> <td>Изм.</td> <td>Лист</td> <td>№ докум.</td> <td>Подп.</td> <td>Дата</td> </tr> <tr> <td>Разраб.</td> <td></td> <td>Ахметова</td> <td></td> <td></td> </tr> <tr> <td>Пров.</td> <td></td> <td></td> <td></td> <td></td> </tr> <tr> <td>Т.контр.</td> <td></td> <td></td> <td></td> <td></td> </tr> <tr> <td>Н.контр.</td> <td></td> <td></td> <td></td> <td></td> </tr> <tr> <td>Утв.</td> <td></td> <td></td> <td></td> <td></td> </tr> </table>				Изм.	Лист	№ докум.	Подп.	Дата	Разраб.		Ахметова			Пров.					Т.контр.					Н.контр.					Утв.					<table border="1" style="width: 100%;"> <tr> <td>Лист</td> <td>Масса</td> <td>Масштаб</td> </tr> <tr> <td>1</td> <td>3,85</td> <td>1:10</td> </tr> <tr> <td>Листов</td> <td>1</td> <td>2</td> </tr> </table>				Лист	Масса	Масштаб	1	3,85	1:10	Листов	1	2
Изм.	Лист	№ докум.	Подп.	Дата	
Разраб.		Ахметова	
Пров.	
Т.контр.	
Н.контр.	
Утв.	
Лист	Масса	Масштаб	
1	3,85	1:10	
Листов	1	2	

ТФРП.401.362281.01.00115-01


ТФРП.401.362281.01.00115-03 – зеркальное отражение

Остальное – см. ТФРП.401.362281.01.00115-01Q,

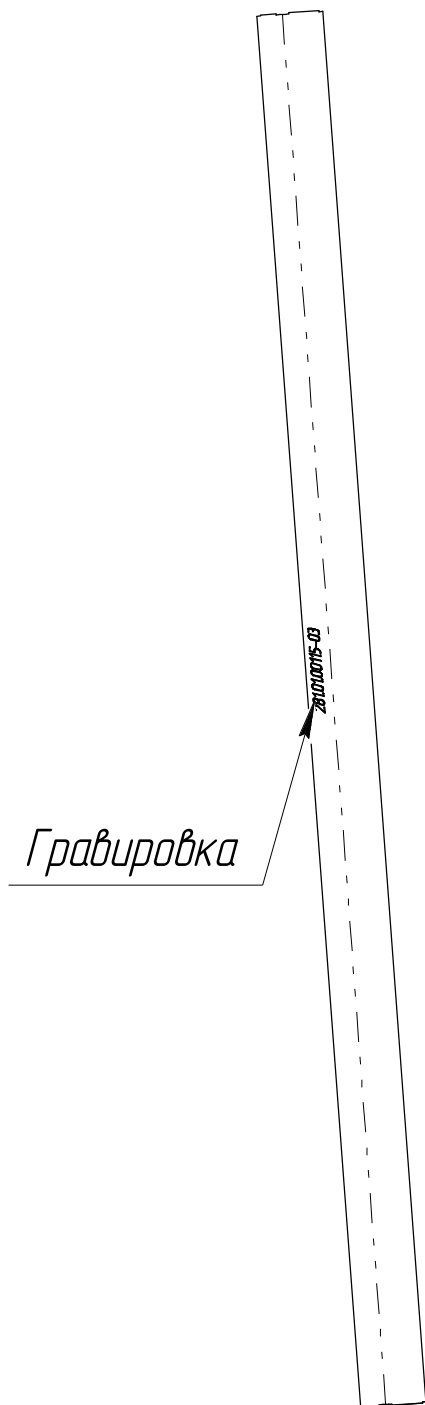

Инв. № подл.	Подп. и дата	Взам. инв. №	Инв. № дубл.	Подп. и дата
Изм.	Лист	№ докум.	Подп.	Дата
ТФРП.401.362281.01.00115-01				
Копировал				Лист
Формат А4				2

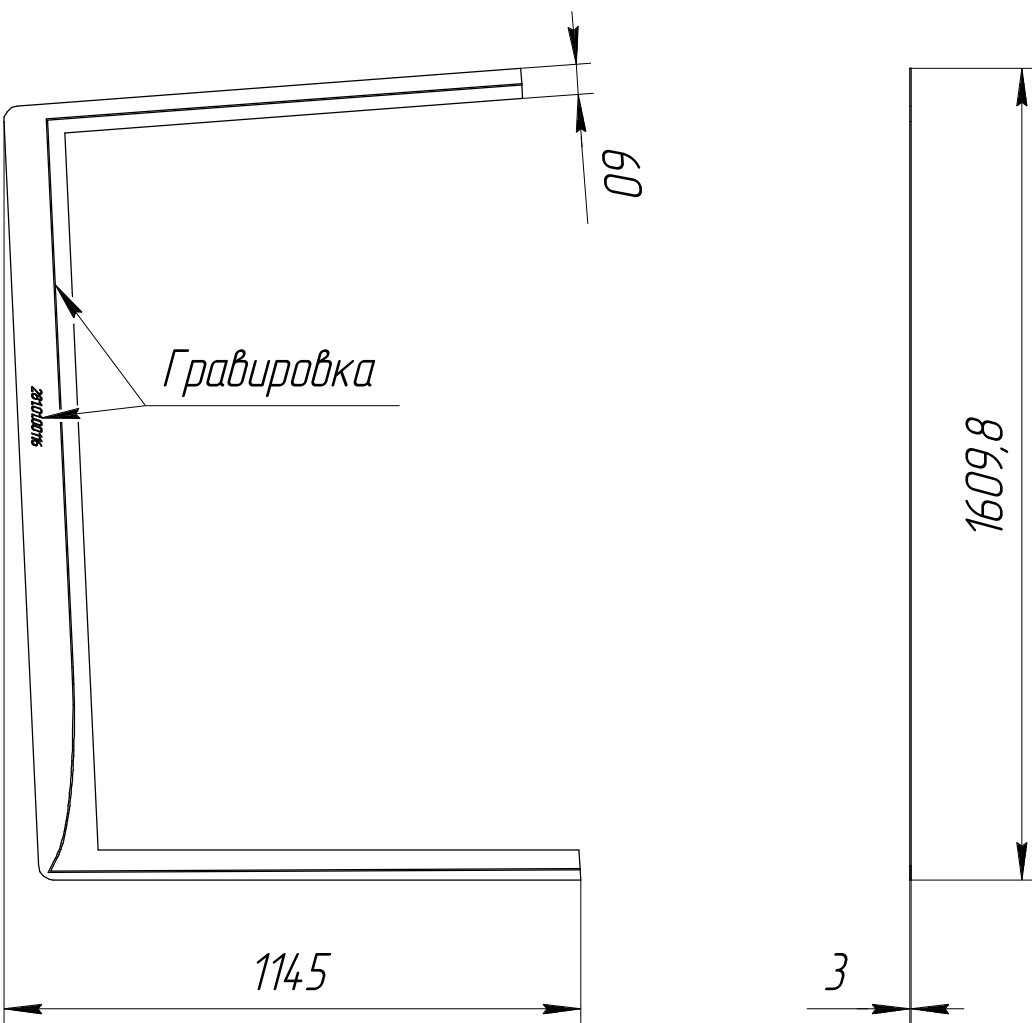


Справ. №		Перв. примен.		ТФРП.401.362281.01.00116				
Инв. № подл.		Подп. и дата		Взам. инв. №		Инв. № дубл.		
Изм. Лист		№ докум.		Подп.		Дата		
Разраб.		Мантров						
Пров.								
Т.контр.								
Н.контр.								ТФРП.401.362281.01.00116  <b>Фланец</b>  Сталь 10 ГОСТ 1050-2013
Утв.								
								Лист 1    Масса 11,8    Масштаб 1:15 Листов 2

ТФРП.401.362281.01.00116

ТФРП.401.362281.01.00116-01 – зеркальное отражение


Остальное – см. ТФРП.401.362281.01.00116

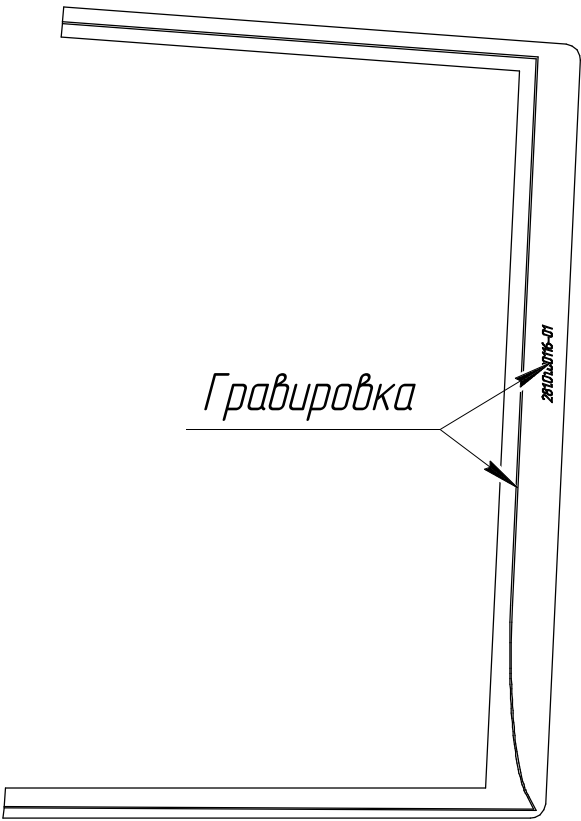

Инв. № подл.	Подп. и дата	Взам. инв. №	Инв. № докл.	Подп. и дата
Изм.	Лист	№ докум.	Подп.	Дата

ТФРП.401.362281.01.00116


Лист  
2

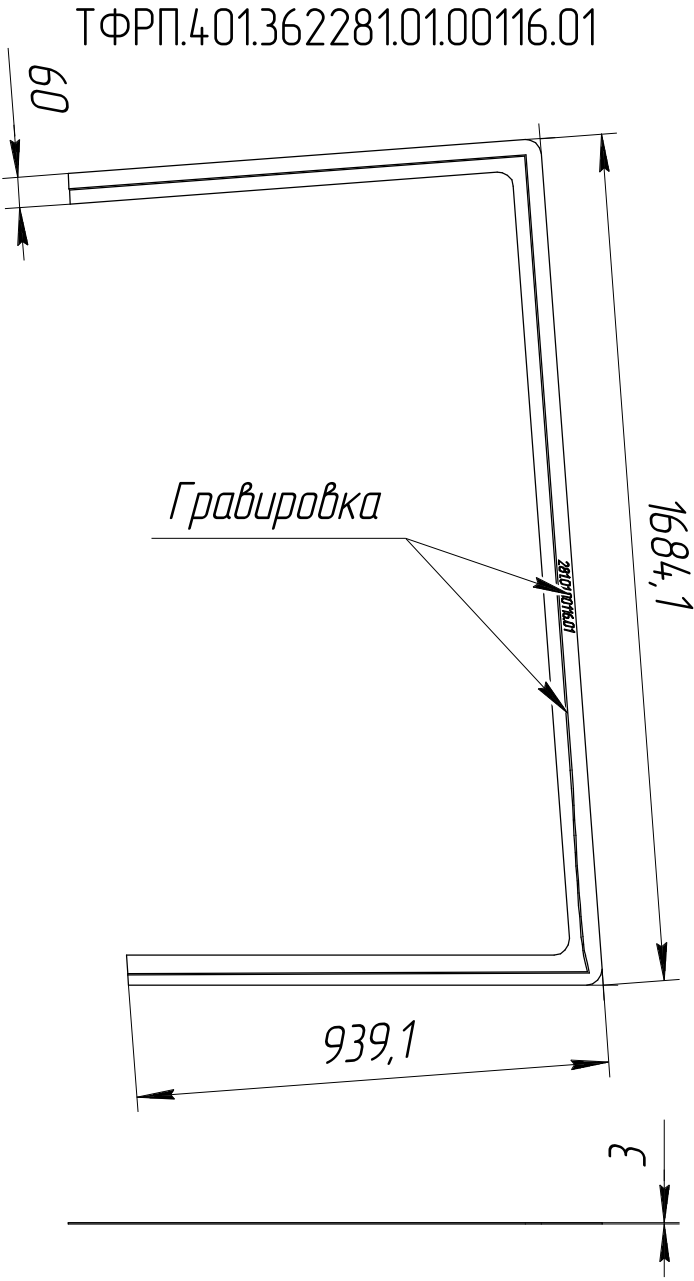Справ. №		Перв. примен.		ТФРП.401.362281.01.00116.01								
Подп. и дата		Взам. инв. №		Инв. № дубл.		Подп. и дата		<div><div>ТФРП.401.362281.01.00116.01</div></div>				
Инв. № подл.		Т.контр.										
Изм. Лист		№ докум.		Подп.		Дата		ТФРП.401.362281.01.00116.01				
Разраб.		Ахметова										
Пров.								Фланец				
Н.контр.												
Утв.								Сталь 10 ГОСТ 1050-2013				
								Лист 1				
								Листов 2				
								Масса 4,84				
								Масштаб 1:15				
								Формат А4				

ТФРП.401.362281.01.00116.01

ТФРП.401.362281.01.00116.01-01 – зеркальное отражение

Остальное – см. ТФРП.401.362281.01.00116.01

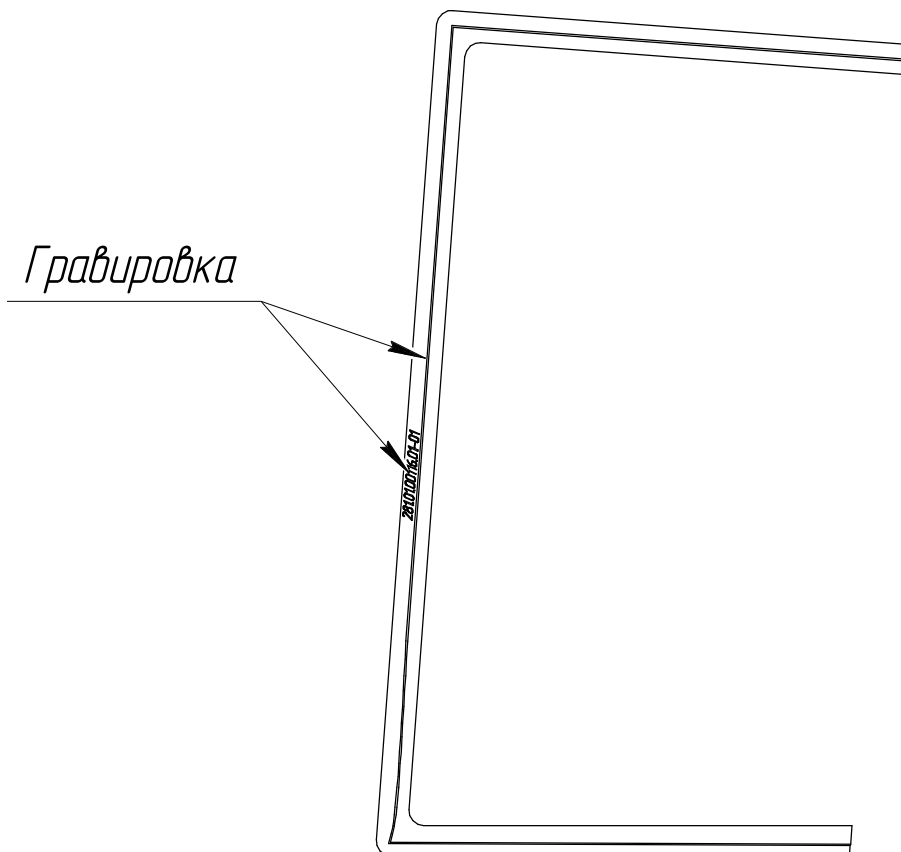

Инв. № подл.	Подп. и дата	Взам. инв. №	Инв. № дубл.	Подп. и дата

Изм.	Лист	№ докум.	Подп.	Дата

ТФРП.401.362281.01.00116.01

Лист  
2

Копировал

Формат А4