

Перв. примен.		Формат	Зона	Поз.	Обозначение	Наименование	Кол.	Приме- чение	
					Переменные данные для исполнений:				
						ТФРП.401.362281.01.0050			
						Детали			
Справ. №		*	1		ТФРП.401.362281.01.0051	Верхняя обечайка	1	*12хА4	
			2		ТФРП.401.362281.01.0051.01	Верхняя обечайка	1		
			3		ТФРП.401.362281.01.0052	Стенка 1	1		
			4		ТФРП.401.362281.01.0053	Стенка 2	1		
			5		ТФРП.401.362281.01.0054	Стенка 3	1		
			6		ТФРП.401.362281.01.0055	Стенка 4	1		
			7		ТФРП.401.362281.01.0056	Фланец	1		
			8		ТФРП.401.362281.01.0056.01	Фланец	1		
		*	9		ТФРП.401.362281.01.0057	Уголок	1	*13хА4	
		*	10		ТФРП.401.362281.01.0057-01	Уголок	1	*13хА4	
						ТФРП.401.362281.01.0050-1			
						Детали			
Взам. инв. №		*	1		ТФРП.401.362281.01.0051-01	Верхняя обечайка	1	*12хА4	
			2		ТФРП.401.362281.01.0051.01-01	Верхняя обечайка	1		
			3		ТФРП.401.362281.01.0052-01	Стенка 1	1		
			4		ТФРП.401.362281.01.0053-01	Стенка 2	1		
			5		ТФРП.401.362281.01.0054-01	Стенка 3	1		
Подп. и дата									
					ТФРП.401.362281.01.0050				
		Изм.	Лист	№ докум.	Подп.	Дата			
Инв. № подл.	Разраб.						Оснастка стекла 5		
	Пров.								
	Н.контр.								
	Утв.								
							Лит.	Лист	Листов
								1	2


[illegible]

Перв. примен.	ТФРП.401.362281.01.0051Q					
	ТФРП.401.362281.01.0051Q					
Справ. №	Гравировка					
Подп. и дата	Инв. № дубл.					
Взам. инв. №	<p>1 Неуказанный внутренний радиусгиба 10 мм</p> <p>2 Проверить по кондуктору ТФРП.401.362281.01.0051-02</p> <p>3 Гравировка снаружи</p>					
Инв. № подл.	Подп. и дата	ТФРП.401.362281.01.0051				
	Изм. Лист	№ докум.	Подп.	Дата		
	Разраб.	Ахметова				
	Пров.					
	Т.контр.					
Н.контр.	Верхняя обечайка			Лист	Масса	Масштаб
				Лист	1	Листов
Утв.	Сталь 10 ГОСТ 1050-2013					


ТФРП.401.362281.01.0051

ТФРП.401.362281.01.0051-01 – зеркальное отражение

Остальное – см. ТФРП.401.362281.01.0051Q,

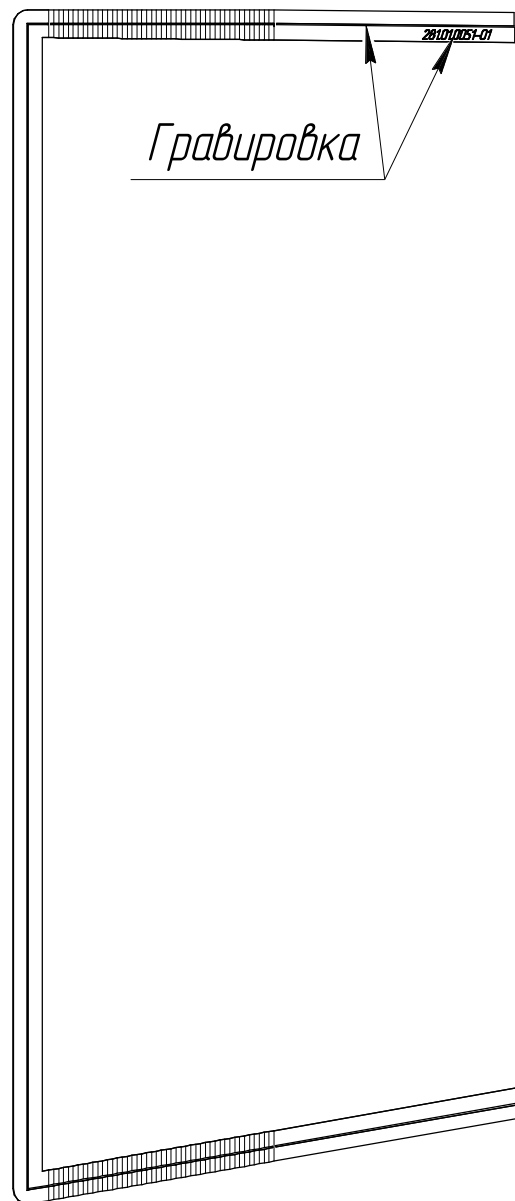

ТФРП.401.362281.01.0051-02 Кондуктор(1:5)

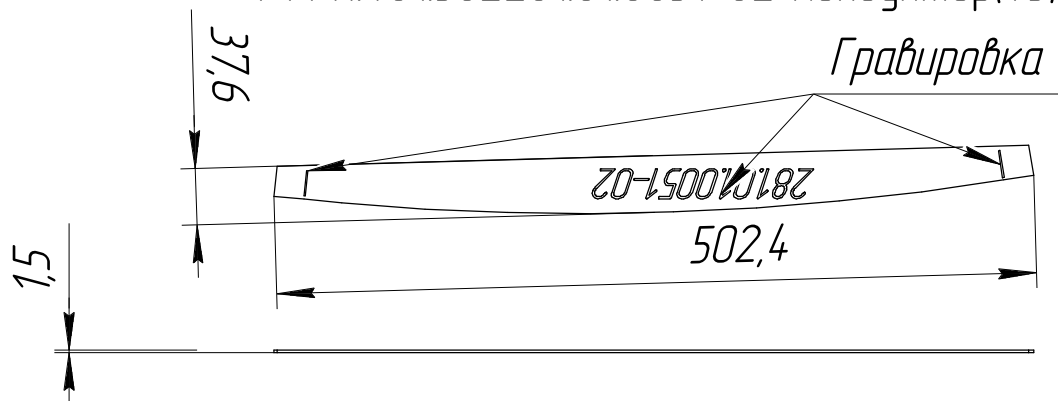

Инв. № подл.	Подп. и дата	Взам. инв. №	Инв. № дубл.	Подп. и дата
Изм.	Лист	№ докум.	Подп.	Дата
ТФРП.401.362281.01.0051				
Копировал				
Формат А4				
Лист				2

Справ. №		Перв. примен.	
Инв. № подл.		Подп. и дата	
Т.контр.		Инв. № докл.	
Н.контр.		Взам. инв. №	
Утв.		Подп. и дата	

ТФРП.401.362281.01.0051.01

ТФРП.401.362281.01.0051.01				
Изм.	Лист	№ докум.	Подп.	Дата
Разраб.	Ахметова			
Пров.				
Т.контр.				
Верхняя обечайка				
Сталь 10 ГОСТ 1050-2013				


Лист	1	Масса	5,81	Масштаб	1:15
Лист	1	Листов	2		

Копировал
Формат А4

ТФРП.401.362281.01.0051.01

ТФРП.401.362281.01.0051.01 – зеркальное отражение

Остальное – см. ТФРП.401.362281.01.0051.01

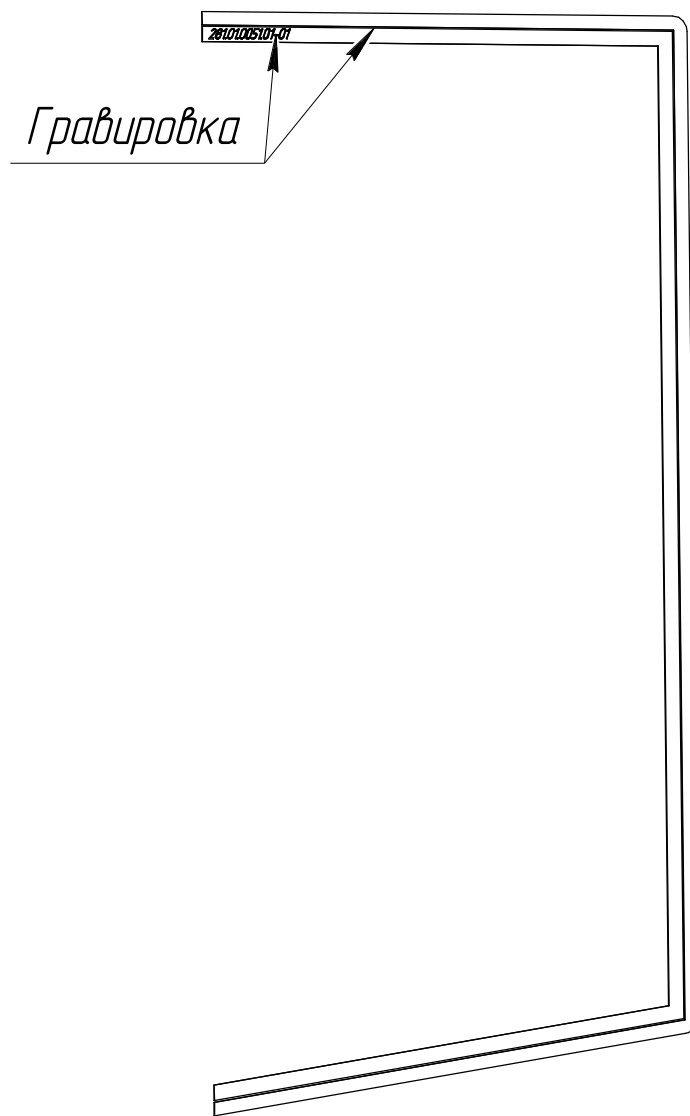

Инв. № подл.	Подп. и дата	Взам. инв. №	Инв. № дубл.	Подп. и дата
Изм.	Лист	№ докум.	Подп.	Дата
ТФРП.401.362281.01.0051.01				
Копировал				Лист
Формат А4				2

Справ. №		Перв. примен.		<div>ТФРП.401.362281.01.0052</div> <div>2016,5</div> <div>400</div> <div>2810052-01</div> <div>Гравировка</div> <div>3</div>	
Подп. и дата		Инв. № дубл.		<div>ТФРП.401.362281.01.0052-01 – зеркальное отражение</div> <div>Остальное – см. ТФРП.401.362281.01.0052</div> <div>Гравировка</div>	
Инв. № подл.		Подп. и дата		<div>ТФРП.401.362281.01.0052</div> <div>Стенка 1</div> <div>Сталь 10 ГОСТ 1050-2013</div>	
Изм. Лист		№ докум.		Лит.	
Разраб.		Ахметова		Масса	
Пров.				11,44	
Т.контр.				Масштаб	
				1:15	
Н.контр.				Лист	
Утв.				Листов 1	


Формат А4



Справ. №	Перв. примен.
----------	---------------


ТФРП.401.362281.01.0054

ТФРП.401.362281.01.0054

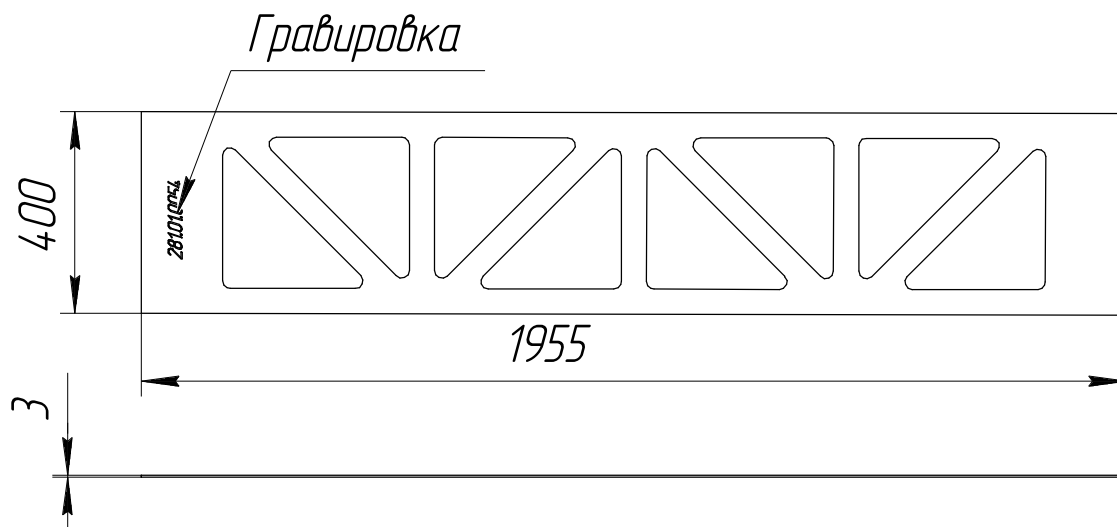

ТФРП.401.362281.01.0054-01 – зеркальное отражение

Остальное – см. ТФРП.401.362281.01.0054

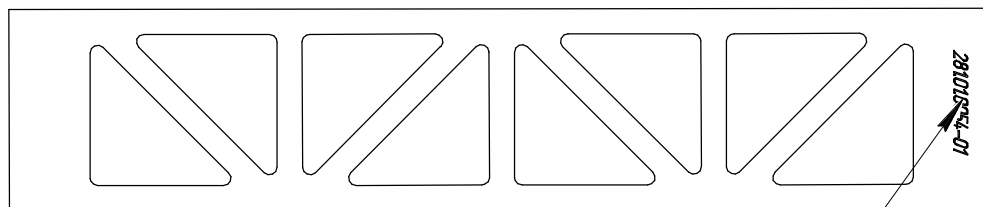


Инв. № подл.	Т.контр.	Пров.	Разраб.	Изм. Лист
Инв. № докл.	Подп. и дата	Взам. инв. №	Инв. № докл.	Подп. и дата

Инв. № подл.	Т.контр.	Пров.	Разраб.	Изм. Лист
Инв. № докл.	Подп. и дата	Взам. инв. №	Инв. № докл.	Подп. и дата

ТФРП.401.362281.01.0054			
Стенка 3			
Сталь 10 ГОСТ 1050-2013			

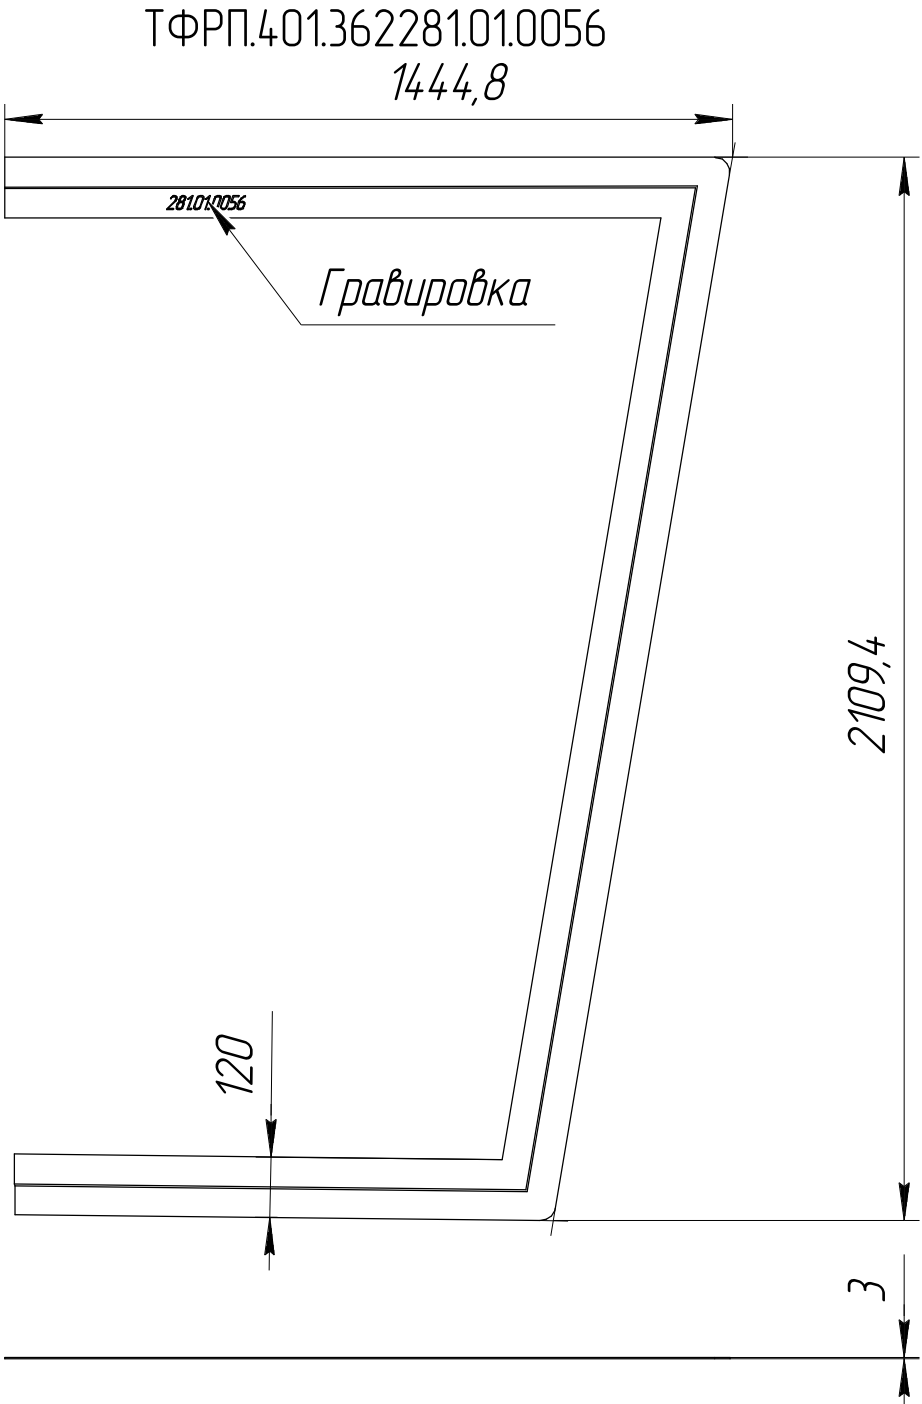

Перв. примен.		Справ. №		Подп. и дата		Взам. инв. №		Инв. № дубл.		Подп. и дата										
ТФРП.401.362281.01.0056																				
						ТФРП.401.362281.01.0056														
						Фланец		<table><tr><td>Лист</td><td>Масса</td><td>Масштаб</td></tr><tr><td></td><td>23,27</td><td>1:15</td></tr><tr><td>Лист 1</td><td>Листов 2</td><td></td></tr></table>				Лист	Масса	Масштаб		23,27	1:15	Лист 1	Листов 2	
Лист	Масса	Масштаб																		
	23,27	1:15																		
Лист 1	Листов 2																			
Инв. № подл.		Подп. и дата		Взам. инв. №		Инв. № дубл.		Подп. и дата		Изм. Лист										
Т.контр.		Н.контр.		Утв.		Сталь 10 ГОСТ 1050-2013														


TPP17401362281010056

ТФРП.401.362281.01.0056-01 – зеркальное отражение

Остальное – см. ТФРП.401.362281.01.0056

Гравировка

**281.010056-01**

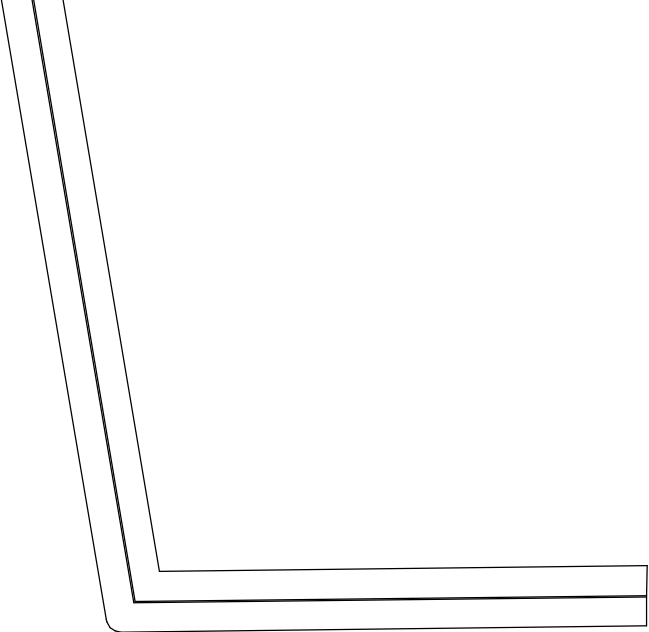
Инв. № подл.	Подп. и дата	Взам. инв. №	Инв. № дудл.	Подп. и дата	
Изм.	Лист	№ докум.	Подп.	Дата	<p>ТФРП.401.362281.01.0056</p>
					<p>Лист</p> <p>2</p>

Справ. №		Перв. примен.		ТФРП.401.362281.01.0056.01										
Подп. и дата		Взам. инв. №		Инв. № дубл.		Подп. и дата		<div><div>ТФРП.401.362281.01.0056.01</div><div><div>281010056.01</div><div>Гравировка</div></div><div>120</div><div>2096,9</div><div>1000</div><div>3</div></div>						
Инв. № подл.	Изм.	Лист	№ докум.	Подп.	Дата	ТФРП.401.362281.01.0056.01				Лист	Масса	Масштаб		
	Разраб.	Ахметова											10,84	1:15
	Пров.													
	Т.контр.													
	Н.контр.					Сталь 10 ГОСТ 1050-2013				Лист	1	Листов	2	
	Утв.													

ТФРП.401.362281.01.0056.01

ТФРП.401.362281.01.0056.01-01 – зеркальное отражение

Остальное – см. ТФРП.401.362281.01.0056.01

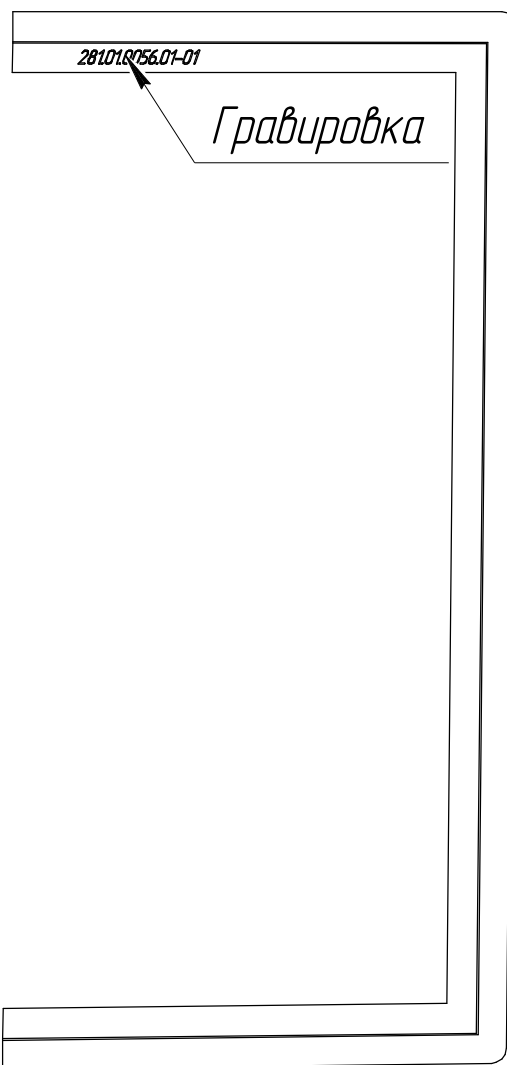

Инв. № подл.	Подп. и дата	Взам. инв. №	Инв. № дубл.	Подп. и дата
Изм.	Лист	№ докум.	Подп.	Дата
ТФРП.401.362281.01.0056.01				
Копировал				
Формат А4				
				Лист
				2


ИНВ. № подл.

ИНВ. № подл.

Формат А4

ТФРП.401.362281.01.0057

ТФРП.401.362281.01.0057-01Q

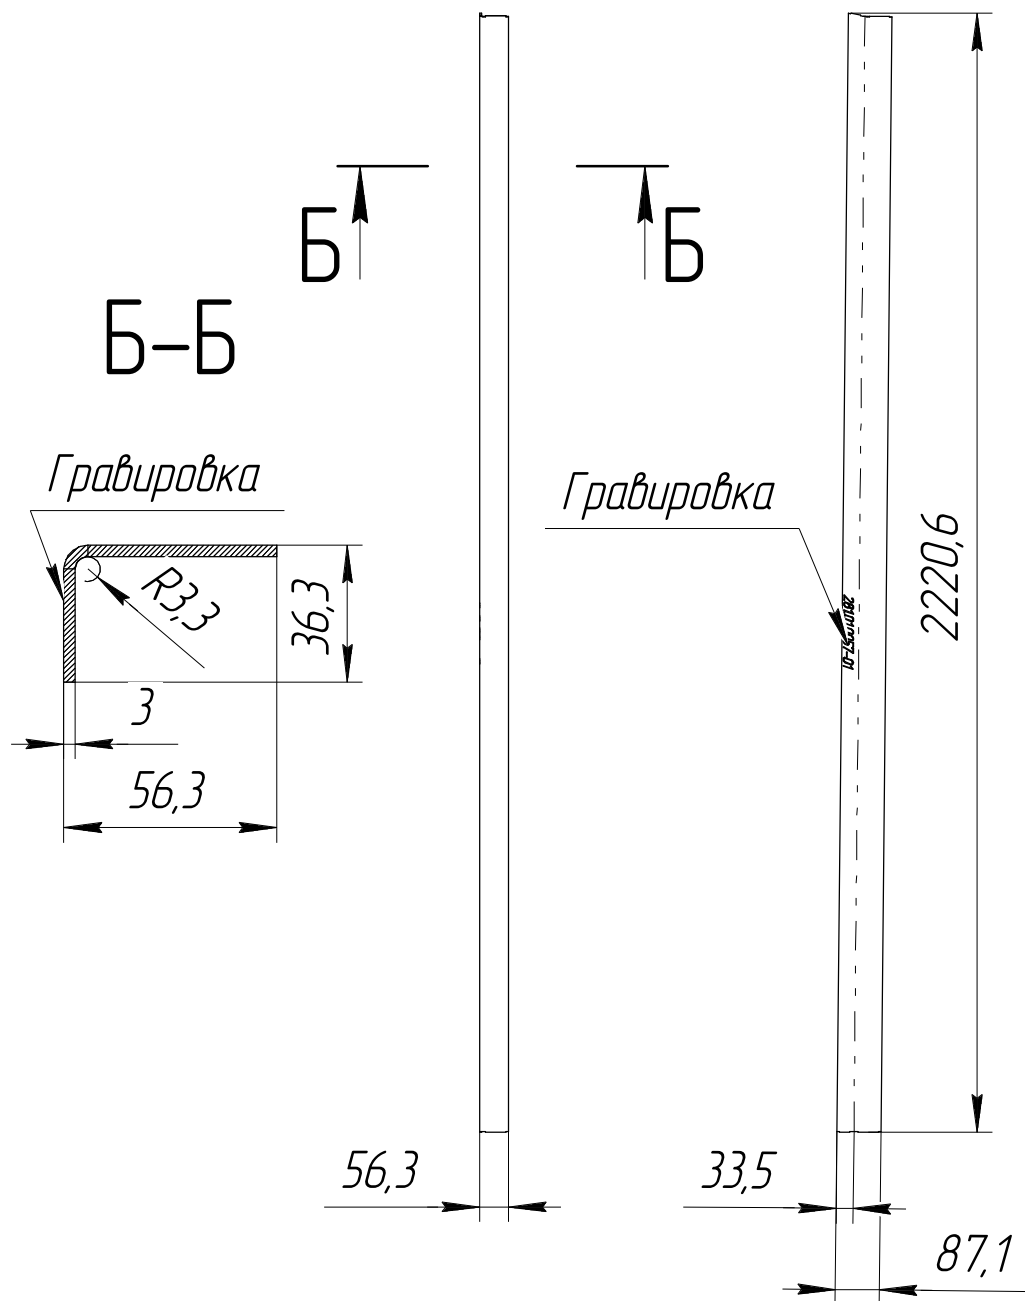

Инв. № подл.	Подп. и дата	Взам. инв. №	Инв. № дудл.	Подп. и дата
Изм.	Лист	№ докум.	Подп.	Дата
ТФРП.401.362281.01.0057				
Копировал				
Формат А4				
				Лист
				2



10001010057

ТФРП.401.362281.01.0057-02 –  
зеркальное отражение  
Остальное – см.  
ТФРП.401.362281.01.0057Q

ТФРП.401.362281.01.0057-03 –  
зеркальное отражение  
Остальное – см.  
ТФРП.401.362281.01.0057-01

Гравировка

Гравировка

Инв. № подл.	Подп. и дата	Взам. инв. №	Инв. № дудл.	Подп. и дата

Грубоприбойка

Изм.	Лист	№ докцм.	Подп.	Дата

ТФРП.401.362281.01.0057

Лист  
3