

Справ. №

Подн. и дама

Инв. № дубл.


ВЗАМ. УНВ. №

Подн. и дата

ИНВ. № подл.

131001013622810100131

ТФРП.401.362281.01.00131Q₂

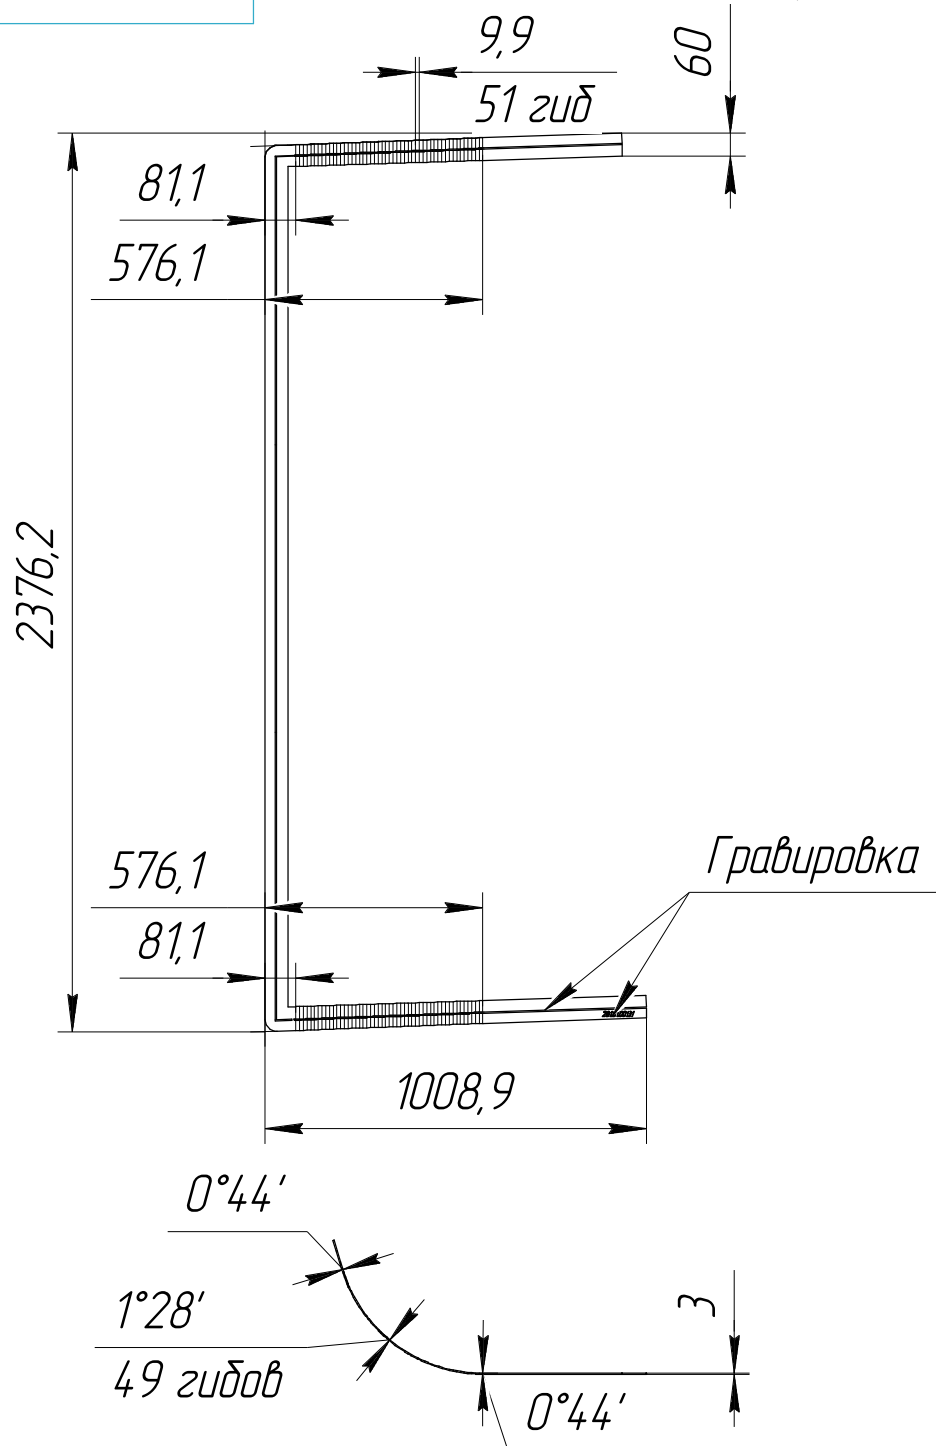

- 1 Неуказанный внутренний радиус гйда 10 мм
2 Гравировка внутри
3 Проверить по кондуктору ТФРП.401.362281.01.00131-02

ТФРП.401.362281.01.00131

Верхняя обечайка

Сталь 10 ГОСТ 1050-2013

Aut.

Macca

Μαριμαδ

5,6

1:20

Луст

↑


Листов

2


ТФРП.401.362281.01.00131

ТФРП.401.362281.01.00131-01 – зеркальное отражение

Остальное – см. ТФРП.401.362281.01.00131Q

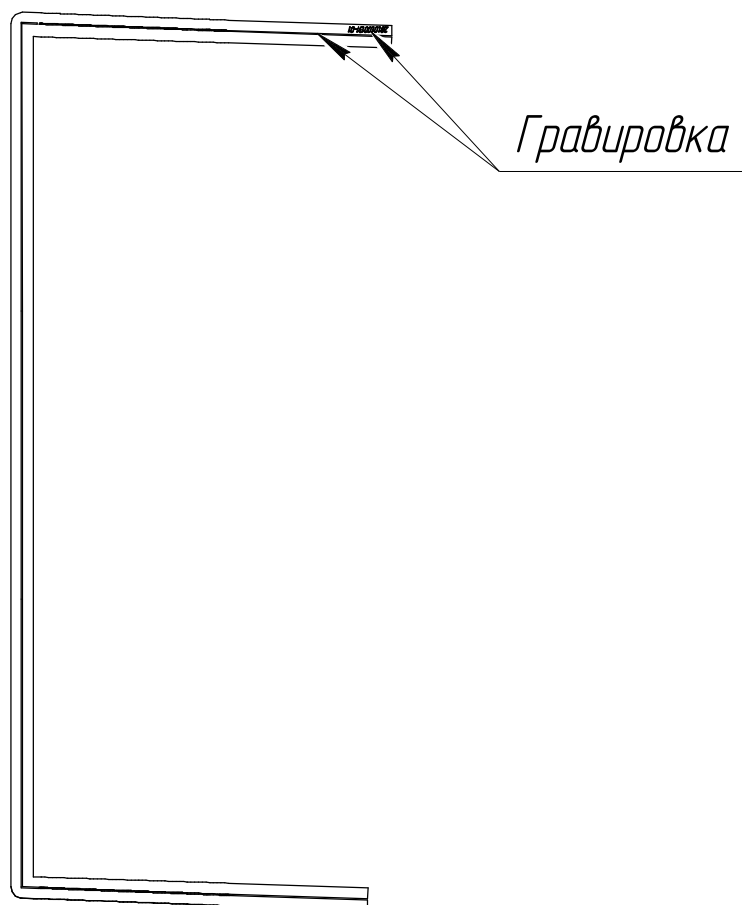

ТФРП.401.362281.01.00131-02 Кондуктор(1:5)

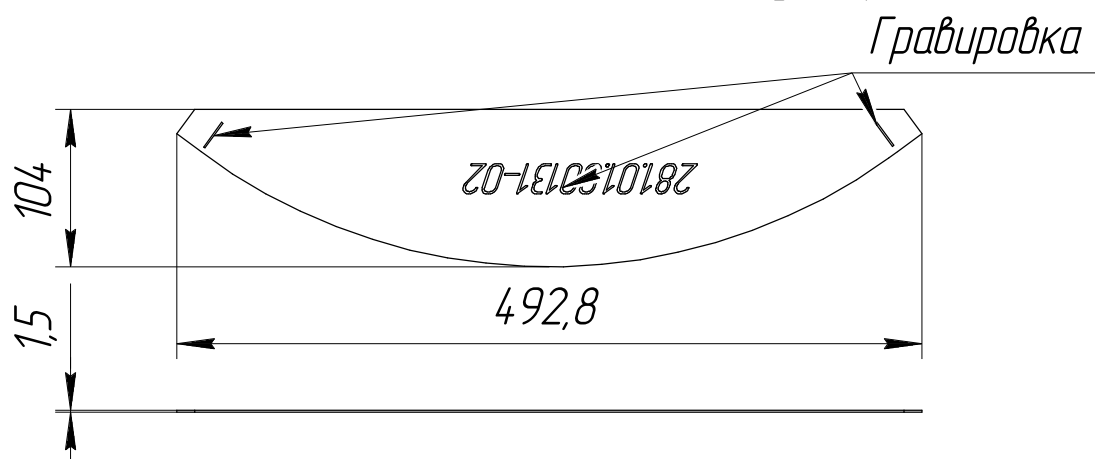

Инв. № подл.	Подп. и дата	Взам. инв. №	Инв. № дубл.	Подп. и дата
Изм.	Лист	№ докум.	Подп.	Дата

ТФРП.401.362281.01.00131


Лист2

Копировал

Формат А4

Инв. № подл.		Подп. и дата	Взам. инв. №	Инв. № дубл.	Подп. и дата	Справ. №	Перв. примен.

ТФРП.401.362281.01.00131.01

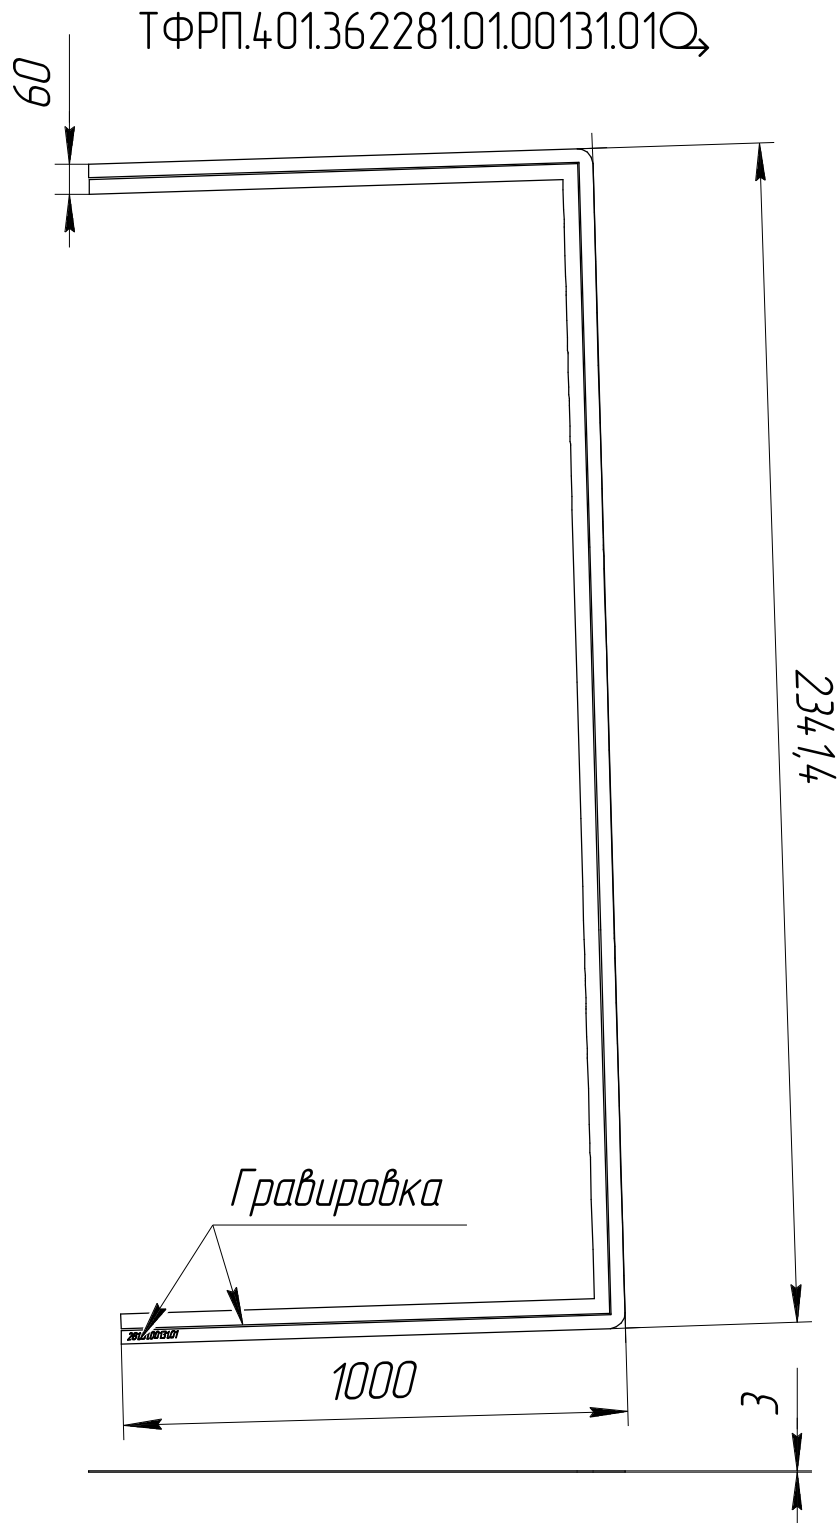

Изм. Лист	№ докум.	Подп.	Дата	
Разраб.	Ахметова			
Пров.				
Т.контр.				
Н.контр.				
Утв.				


ТФРП.401.362281.01.00131.01			
Верхняя обечайка			
Сталь 10 ГОСТ 1050-2013			

Лист	Масса	Масштаб
1	5,66	1:15
Лист	1	Листов 2

ТФРП.401.362281.01.00131.01

ТФРП.401.362281.01.00131.01-01 – зеркальное отражение

Остальное – см. ТФРП.401.362281.01.00131.01


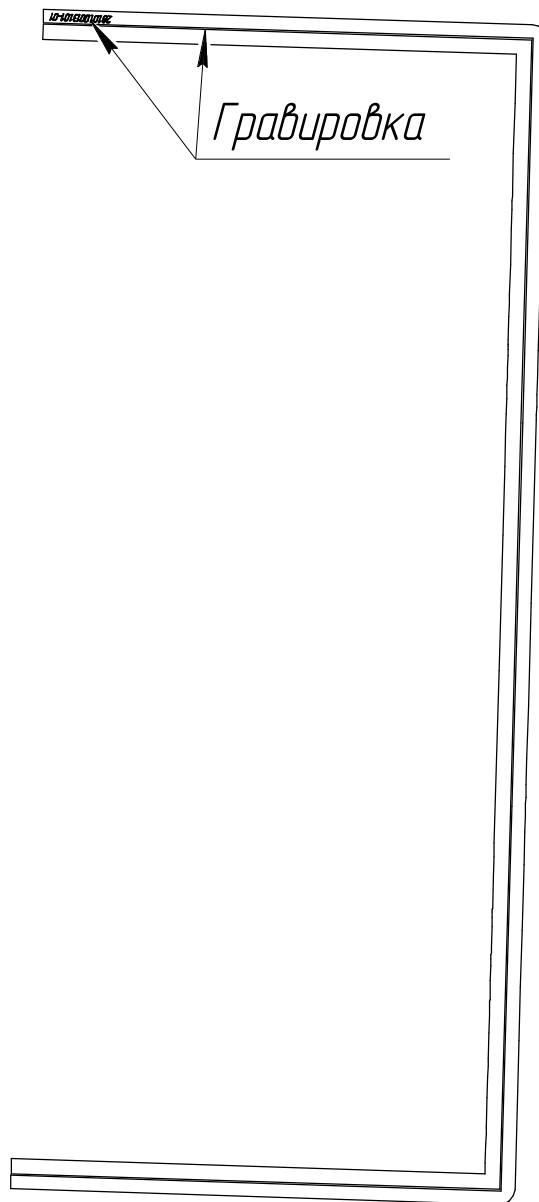


Инв. № подл.	Подп. и дата	Взам. инв. №	Инв. № дубл.	Подп. и дата
Изм.	Лист	№ докум.	Подп.	Дата
ТФРП.401.362281.01.00131.01				
Копировал				Лист
Формат А4				2

ТФРП.401.362281.01.00132


ТФРП.401.362281.01.00132

Гравировка

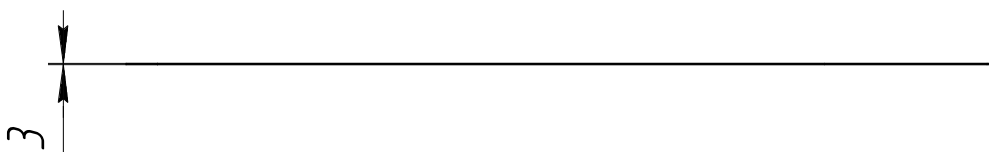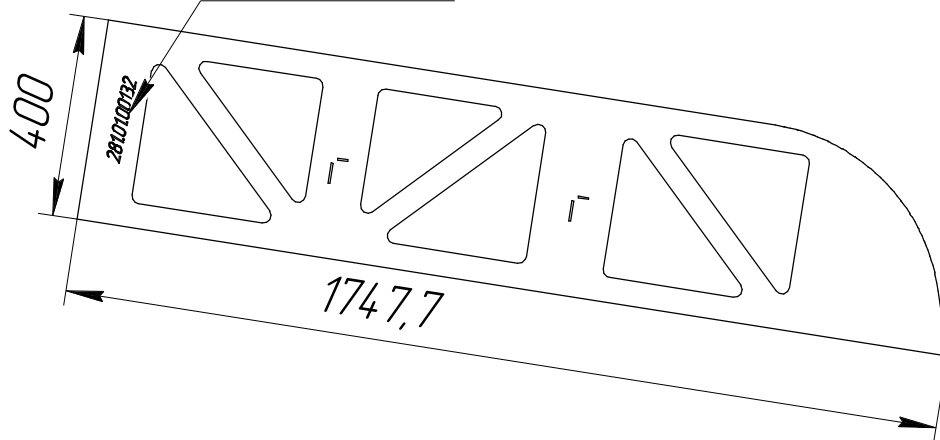

ТФРП.401.362281.01.00132-01 – зеркальное отражение

Остальное – см. ТФРП.401.362281.01.00132

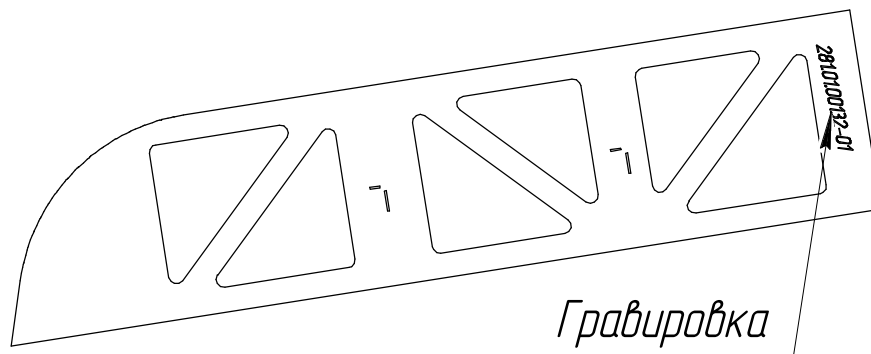

Изм. Лист	№ докум.	Подп.	Дата	
Разраб.	Ахметова			
Пров.				
Т.контр.				
Н.контр.				
Утв.				

ТФРП.401.362281.01.00132

Стенка 1

Сталь 10 ГОСТ 1050-2013

Лист	Масса	Масштаб
	9,65	1:15
Лист	Листов	1


Справ. №		Перв. примен.		ТФРП.401.362281.01.00133	
<p>ТФРП.401.362281.01.00133-01 – зеркальное отражение</p> <p>Остальное – см. ТФРП.401.362281.01.00133</p>					
Подп. и дата		Взам. инв. №		Инв. № докл.	
Подп. и дата		Взам. инв. №		Инв. № докл.	
Инв. № подл.		Т.контр.		Н.контр.	
Изм. Лист		№ докум.		Подп.	
Разраб.		Ахметова		Дата	
Пров.					
Утв.					
ТФРП.401.362281.01.00133				Лит.	
Стенка 2				Масса	
Сталь 10 ГОСТ 1050-2013				Масштаб	
				10,25	
				1:15	
				Лист	
				Листов	
				1	

Справ. №	<div data-bbox="159 33 678 145" data-label="Text"> <p>ТФРП.401.362281.01.00134</p> </div> <div data-bbox="590 145 1077 201" data-label="Text"> <p>ТФРП.401.362281.01.00134</p> </div> <div data-bbox="215 224 1476 963" data-label="Image"> </div> <div data-bbox="375 952 1420 1019" data-label="Text"> <p>ТФРП.401.362281.01.00134-01 – зеркальное отражение</p> </div> <div data-bbox="375 1052 1197 1120" data-label="Text"> <p>Остальное – см. ТФРП.401.362281.01.00134</p> </div> <div data-bbox="223 1131 1412 1545" data-label="Image"> </div>	
Подп. и дата	<div data-bbox="750 1803 1444 1881" data-label="Text"> <p>ТФРП.401.362281.01.00134</p> </div> <div data-bbox="718 1937 1085 2049" data-label="Text"> <p>Стенка 3</p> </div> <div data-bbox="638 2105 1173 2184" data-label="Text"> <p>Сталь 10 ГОСТ 1050-2013</p> </div>	
Инв. № подл.	<table border="1"> <tr> <td data-bbox="151 1780 279 1937">Изм. Лист</td> <td data-bbox="279 1780 454 1937">№ докум.</td> <td data-bbox="454 1780 566 1937">Подп.</td> <td data-bbox="566 1780 646 1937">Дата</td> <td colspan="4" data-bbox="646 1780 1556 1892"></td> </tr> <tr> <td data-bbox="151 1937 279 2004">Разраб.</td> <td data-bbox="279 1937 454 2004">Ахметова</td> <td data-bbox="454 1937 566 2004"></td> <td data-bbox="566 1937 646 2004"></td> <td colspan="4" data-bbox="646 1892 1173 2094" rowspan="3"></td> </tr> <tr> <td data-bbox="151 2004 279 2049">Пров.</td> <td data-bbox="279 2004 454 2049"></td> <td data-bbox="454 2004 566 2049"></td> <td data-bbox="566 2004 646 2049"></td> </tr> <tr> <td data-bbox="151 2049 279 2094">Т.контр.</td> <td data-bbox="279 2049 454 2094"></td> <td data-bbox="454 2049 566 2094"></td> <td data-bbox="566 2049 646 2094"></td> </tr> <tr> <td data-bbox="151 2094 279 2139">Н.контр.</td> <td data-bbox="279 2094 454 2139"></td> <td data-bbox="454 2094 566 2139"></td> <td data-bbox="566 2094 646 2139"></td> <td colspan="4" data-bbox="646 2094 1173 2206" rowspan="2"></td> </tr> <tr> <td data-bbox="151 2139 279 2206">Утв.</td> <td data-bbox="279 2139 454 2206"></td> <td data-bbox="454 2139 566 2206"></td> <td data-bbox="566 2139 646 2206"></td> </tr> </table> <table border="1"> <tr> <td data-bbox="1173 1892 1284 1937">Лит.</td> <td data-bbox="1284 1892 1420 1937">Масса</td> <td data-bbox="1420 1892 1556 1937">Масштаб</td> </tr> <tr> <td data-bbox="1173 1937 1284 2049"></td> <td data-bbox="1284 1937 1420 2049">11,01</td> <td data-bbox="1420 1937 1556 2049">1:15</td> </tr> <tr> <td data-bbox="1173 2049 1332 2094">Лист</td> <td data-bbox="1332 2049 1556 2094">Листов</td> <td data-bbox="1500 2049 1556 2094">1</td> </tr> </table>	Изм. Лист	№ докум.	Подп.	Дата					Разраб.	Ахметова							Пров.				Т.контр.				Н.контр.								Утв.				Лит.	Масса	Масштаб		11,01	1:15	Лист	Листов	1
Изм. Лист	№ докум.	Подп.	Дата	
Разраб.	Ахметова	
Пров.	
Т.контр.	
Н.контр.	
Утв.	
Лит.	Масса	Масштаб	
	11,01	1:15	
Лист	Листов	1	

ТФРП.401.362281.01.00135

ТФРП.401.362281.01.00135-01 – зеркальное отражение

Остальное – см. ТФРП.401.362281.01.00135

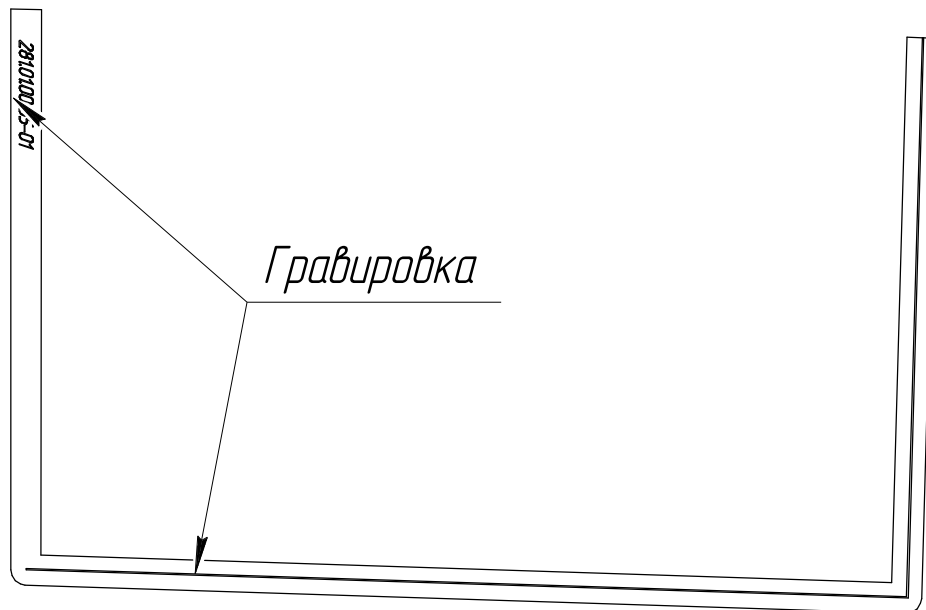



Инв. № подл.	Подп. и дата	Взам. инв. №	Инв. № дубл.	Подп. и дата
Изм.	Лист	№ докум.	Подп.	Дата
ТФРП.401.362281.01.00135				Лист
Копировал				2
Формат А4				

Справ. №		Перв. примен.		ТФРП.401.362281.01.00136					
Инв. № подл.		Т.контр.		Взам. инв. №		Инв. № дубл.		Подп. и дата	
Инв. № подл.		Т.контр.		Взам. инв. №		Инв. № дубл.		Подп. и дата	
Н.контр.		Утв.		Изм. Лист		№ докум.		Подп. Дата	
				Разраб.		Ахметова			
				Пров.					
				Сталь 10		ГОСТ 1050-2013			
				Угол		Лист 1		Листов 3	
				Масса		4,7		Масштаб 1:15	
				Лист		1		Листов 3	

ТФРП.401.362281.01.00136Q

ТФРП.401.362281.01.00136

ТФРП.401.362281.01.00136-01Q

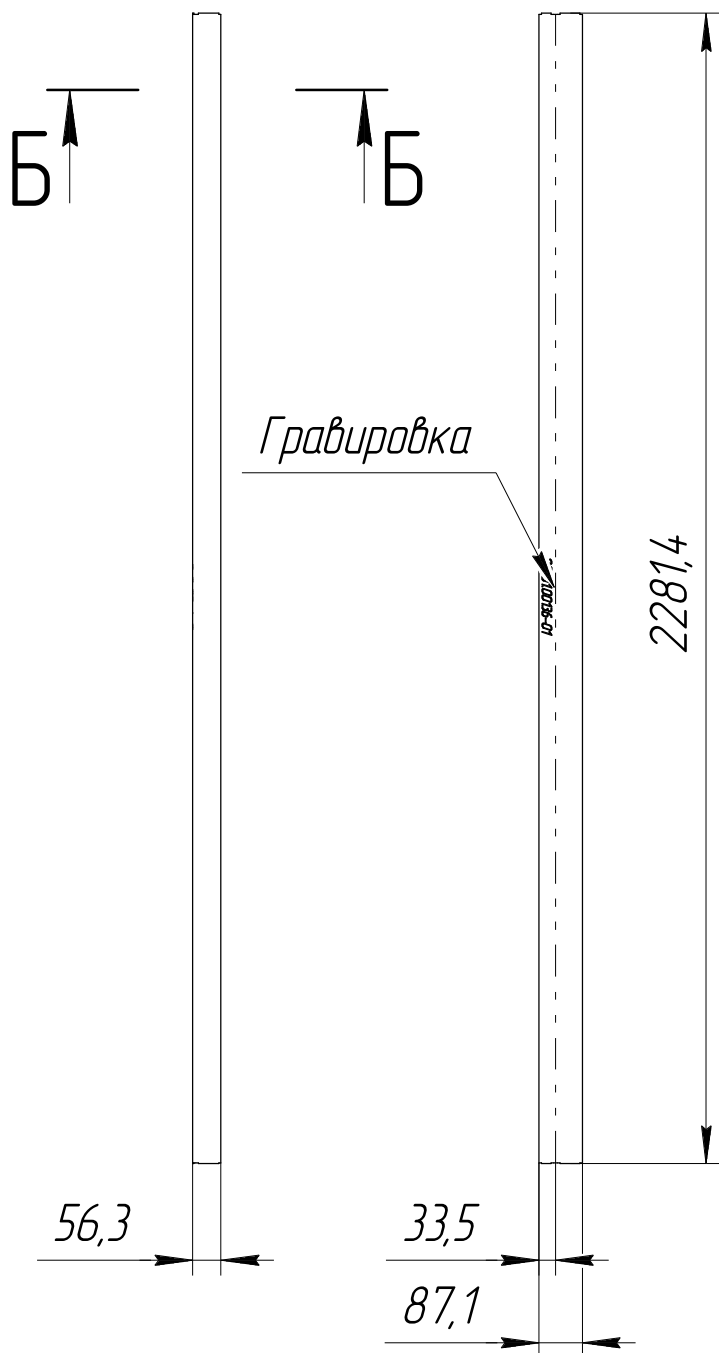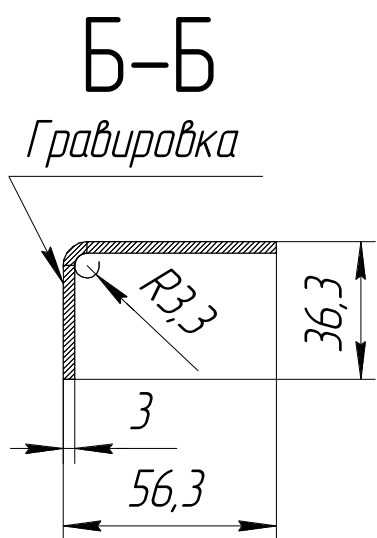

Инв. № подл.	Подп. и дата	Взам. инв. №	Инв. № дубл.	Подп. и дата
Изм.	Лист	№ докум.	Подп.	Дата
ТФРП.401.362281.01.00136				
Копировал				Лист
Формат А4				2

