

Перв. примен.		Формат	Зона	Поз.	Обозначение	Наименование	Кол.	Примечание
					Переменные данные для исполнений:			
						ТФРП.401.362281.01.00100		
						Детали		
Справ. №		*)		1	ТФРП.401.362281.01.00101	Верхняя обечайка	1	*)2хА4
				2	ТФРП.401.362281.01.00101.01	Верхняя обечайка	1	
	А4			3	ТФРП.401.362281.01.00102	Стенка 1	1	
	*)			4	ТФРП.401.362281.01.00103	Стенка 2	1	*)2хА4
	*)			5	ТФРП.401.362281.01.00104	Стенка 3	1	*)2хА4
	*)			6	ТФРП.401.362281.01.00105	Фланец	1	*)2хА4
	*)			7	ТФРП.401.362281.01.00105.01	Фланец	1	*)2хА4
	*)			8	ТФРП.401.362281.01.00106	Уголок	1	*)2хА4
						ТФРП.401.362281.01.00100-1		
						Детали		
Взам. инв. №				1	ТФРП.401.362281.01.00101-01	Верхняя обечайка	1	
				2	ТФРП.401.362281.01.00101.01-01	Верхняя обечайка	1	
	А4			3	ТФРП.401.362281.01.00102-01	Стенка 1	1	
				4	ТФРП.401.362281.01.00103-01	Стенка 2	1	
				5	ТФРП.401.362281.01.00104-01	Стенка 3	1	
	*)			6	ТФРП.401.362281.01.00105-01	Фланец	1	*)2хА4
	*)			7	ТФРП.401.362281.01.00105.01-01	Фланец	1	*)2хА4
Инв. № подл.						<div>ТФРП.401.362281.01.00100</div> <div>Оснастка стекла</div> <div>10</div>		
	Изм.	Лист	№ докум.	Подп.	Дата			
	Разраб.							
	Пров.							
Инв. № подл.						<div>Лит.</div> <div>Лист</div> <div>Листов</div>		
	Н.контр.					<div>1</div> <div>2</div>		
	Утв.							

[illegible]

Перв. примен.	ТФРП.401.362281.01.0010101			
Справ. №				
Подп. и дата				
Инв. № дубл.				
Взам. инв. №				
Подп. и дата				
Инв. № подл.				

ТФРП.401.362281.01.0010101Q

1 Неуказанный внутренний радиус гуда 10 мм  
 2 Проверить по кондуктору ТФРП.401.362281.01.00101-02

					ТФРП.401.362281.01.00101			
Изм.	Лист	№ докум.	Подп.	Дата	Верхняя обечайка			
Разраб.		Ахметова						
Пров.								
Т.контр.								
Н.контр.					Сталь 10 ГОСТ 1050-2013			
Утв.								


Лист		Масса		Масштаб			
		5,41		1:20			
Лист	1	Листов	2				

Копировал
Формат А4


ТФРП.401.362281.01.00101

ТФРП.401.362281.01.00101-01 – зеркальное отражение


Остальное – см. ТФРП.401.362281.01.00101Q

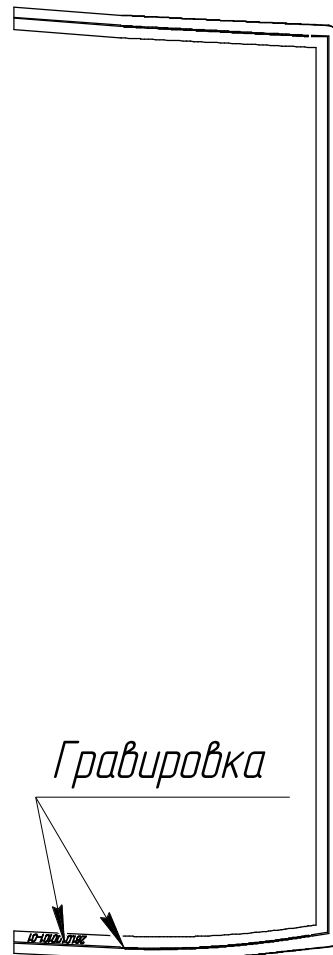

ТФРП.401.362281.01.00101-02 Кондуктор(1:5)

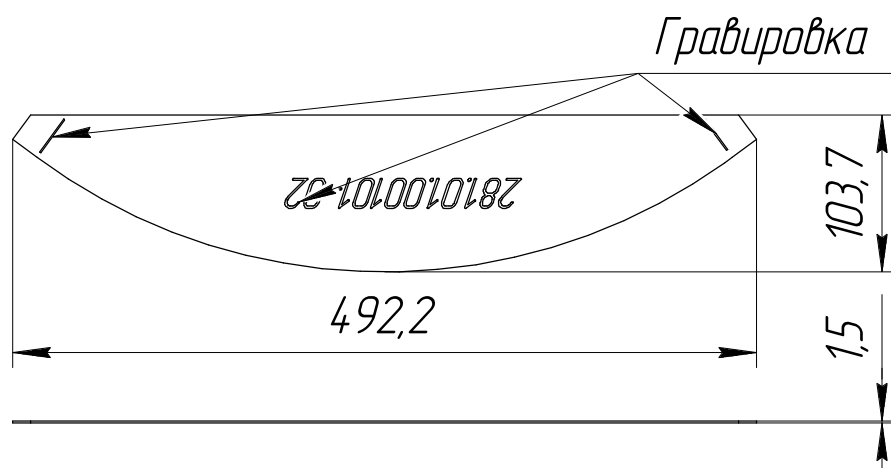


Инв. № подл.	Подп. и дата	Взам. инв. №	Инв. № дубл.	Подп. и дата
Изм.	Лист	№ докум.	Подп.	Дата
ТФРП.401.362281.01.00101				
Копировал				
Формат А4				
				Лист
				2

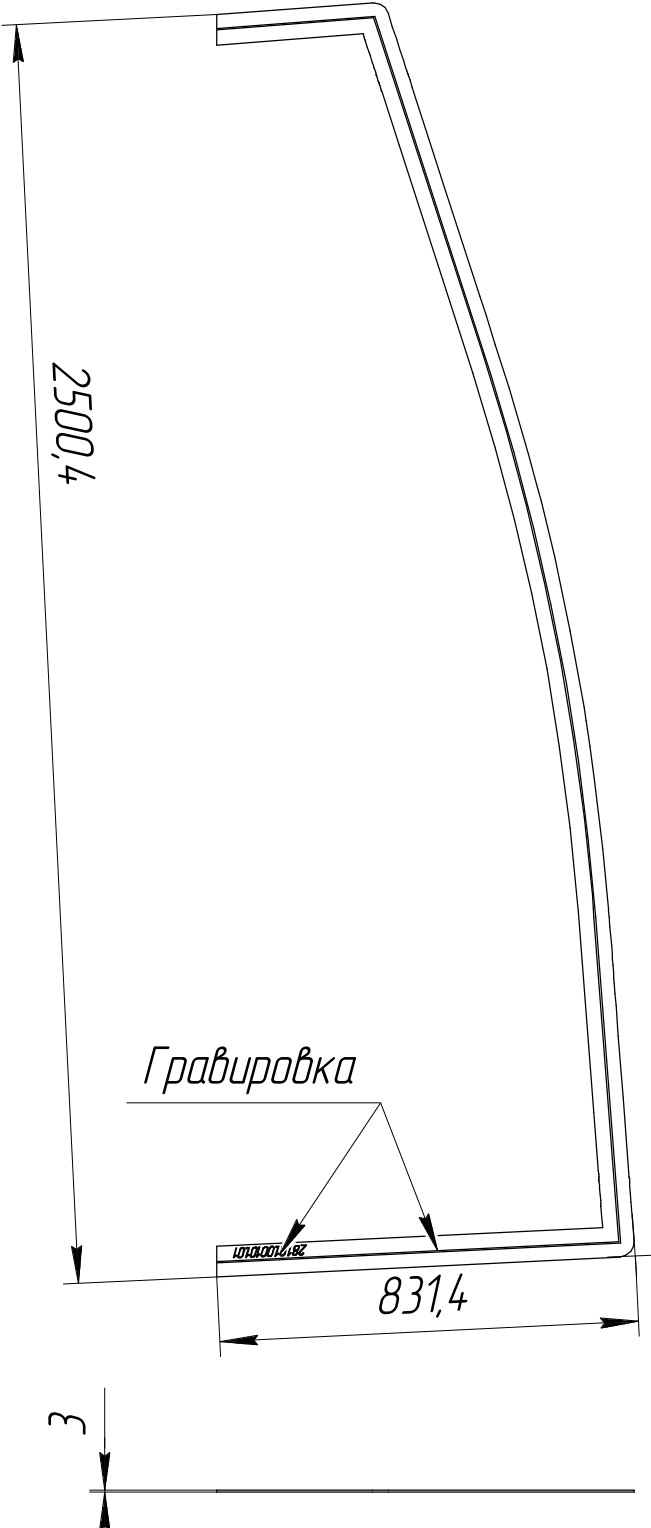Справ. №		Перв. примен.		ТФРП.401.362281.01.00101.01					ТФРП.401.362281.01.00101.01				
													
									ТФРП.401.362281.01.00101.01				
									Верхняя обечайка				
									Сталь 10 ГОСТ 1050-2013				
									Копировал				
									Формат А4				

ТФРП.401.362281.01.00101.01

ТФРП.401.362281.01.00101.01-01 – зеркальное отражение

Остальное – см. ТФРП.401.362281.01.00101.01

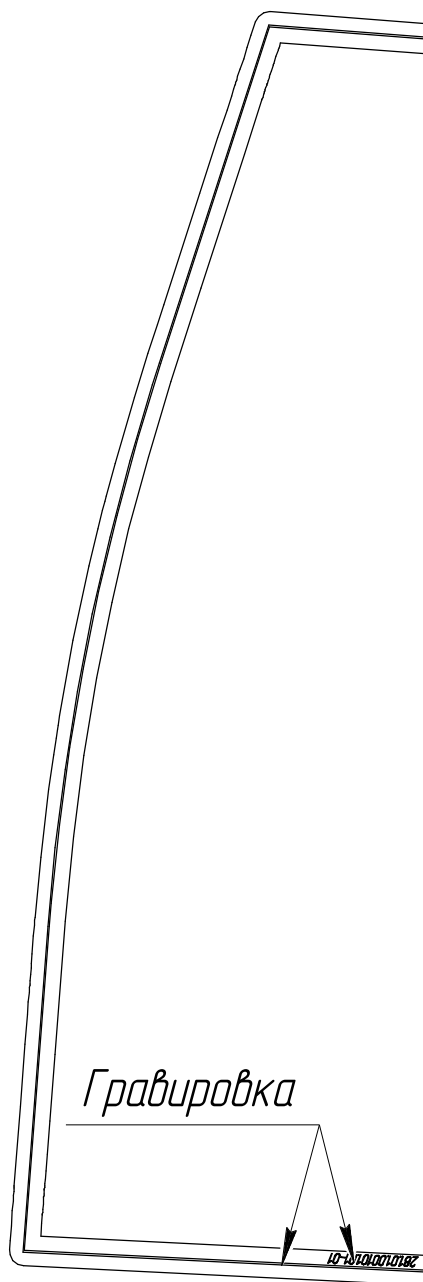


Инв. № подл.	Подп. и дата	Взам. инв. №	Инв. № дубл.	Подп. и дата
Изм.	Лист	№ докум.	Подп.	Дата
ТФРП.401.362281.01.00101.01				Лист
				2

TϕP74013622810100102

ТФРП.401.362281.01.00102


Гравировка

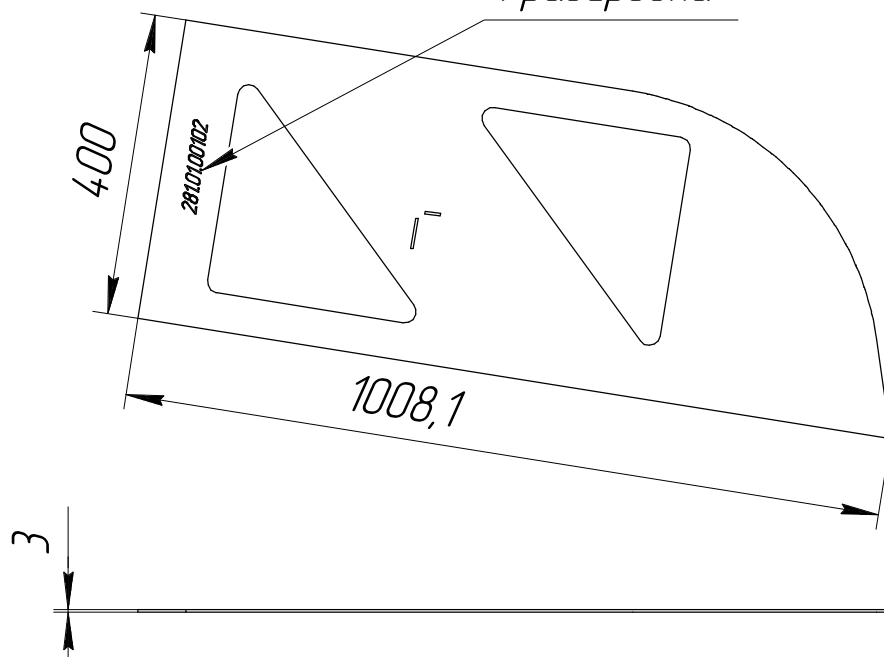

ТФРП.401.362281.01.00102-01 – зеркальное отражение

Остальное – см. ТФРП.401.362281.01.00102

Гравировка

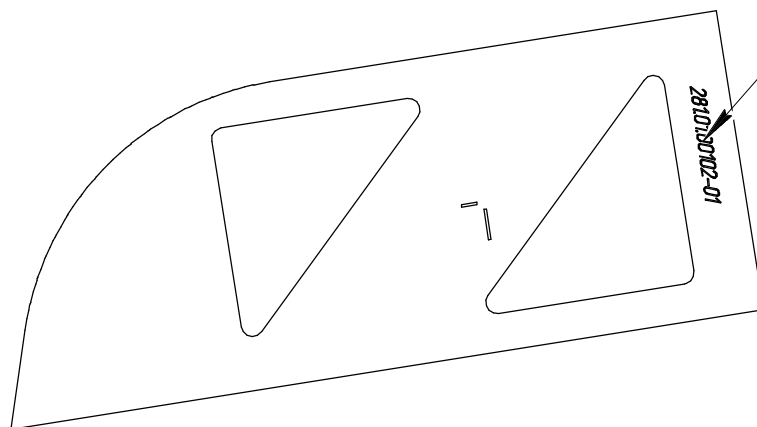

					ТФРП.401.362281.01.00102							
					Стенка 1				Лит.		Масса	Масштаб
Изм.	Лист	№ докум.	Подп.	Дата							6,46	1:10
Разраб.	Ахметова											
Пров.												
Т.контр.									Лист		Листов	
					Сталь 10 ГОСТ 1050-2013							
Н.контр.												
Утв.												








ТФРП.401.362281.01.00103

ТФРП.401.362281.01.00103-01 – зеркальное отражение

Остальное – см. ТФРП.401.362281.01.00103Q,

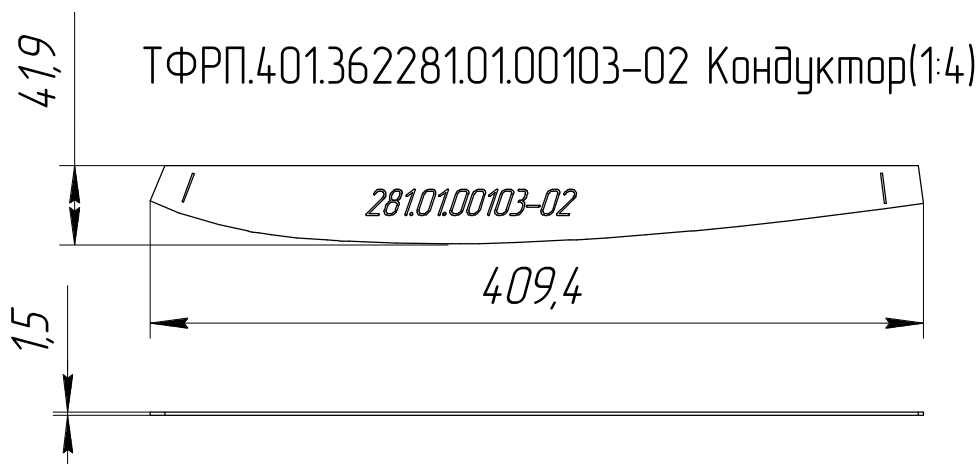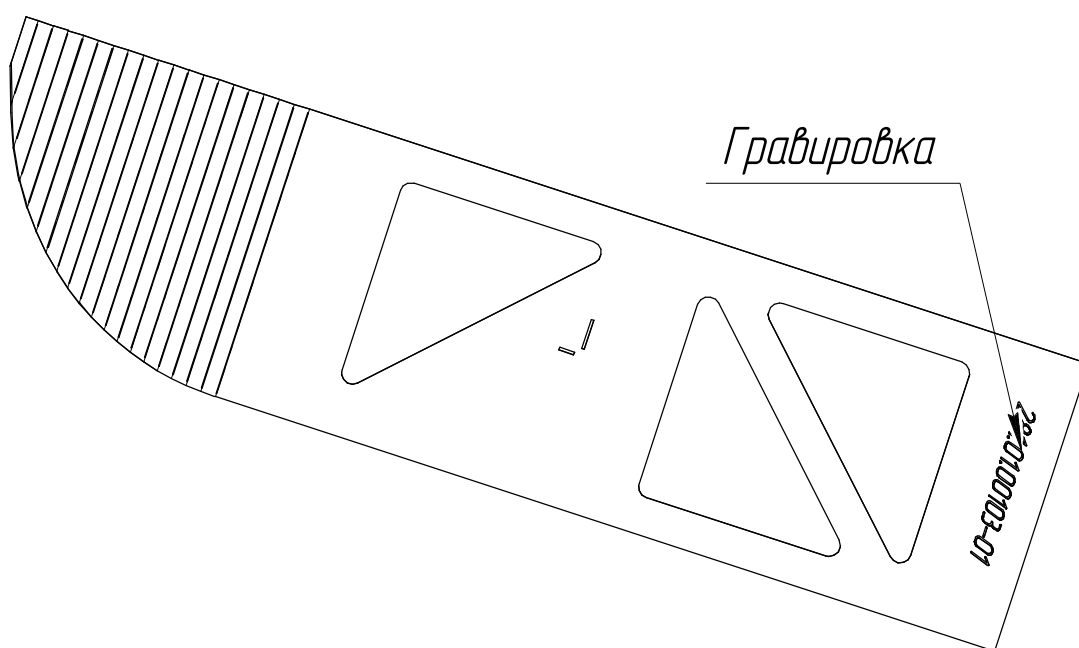


Инв. № подл.	Подп. и дата	Взам. инв. №	Инв. № дубл.	Подп. и дата
Изм.	Лист	№ докум.	Подп.	Дата
ТФРП.401.362281.01.00103				Лист
Копировал				2
Формат А4				

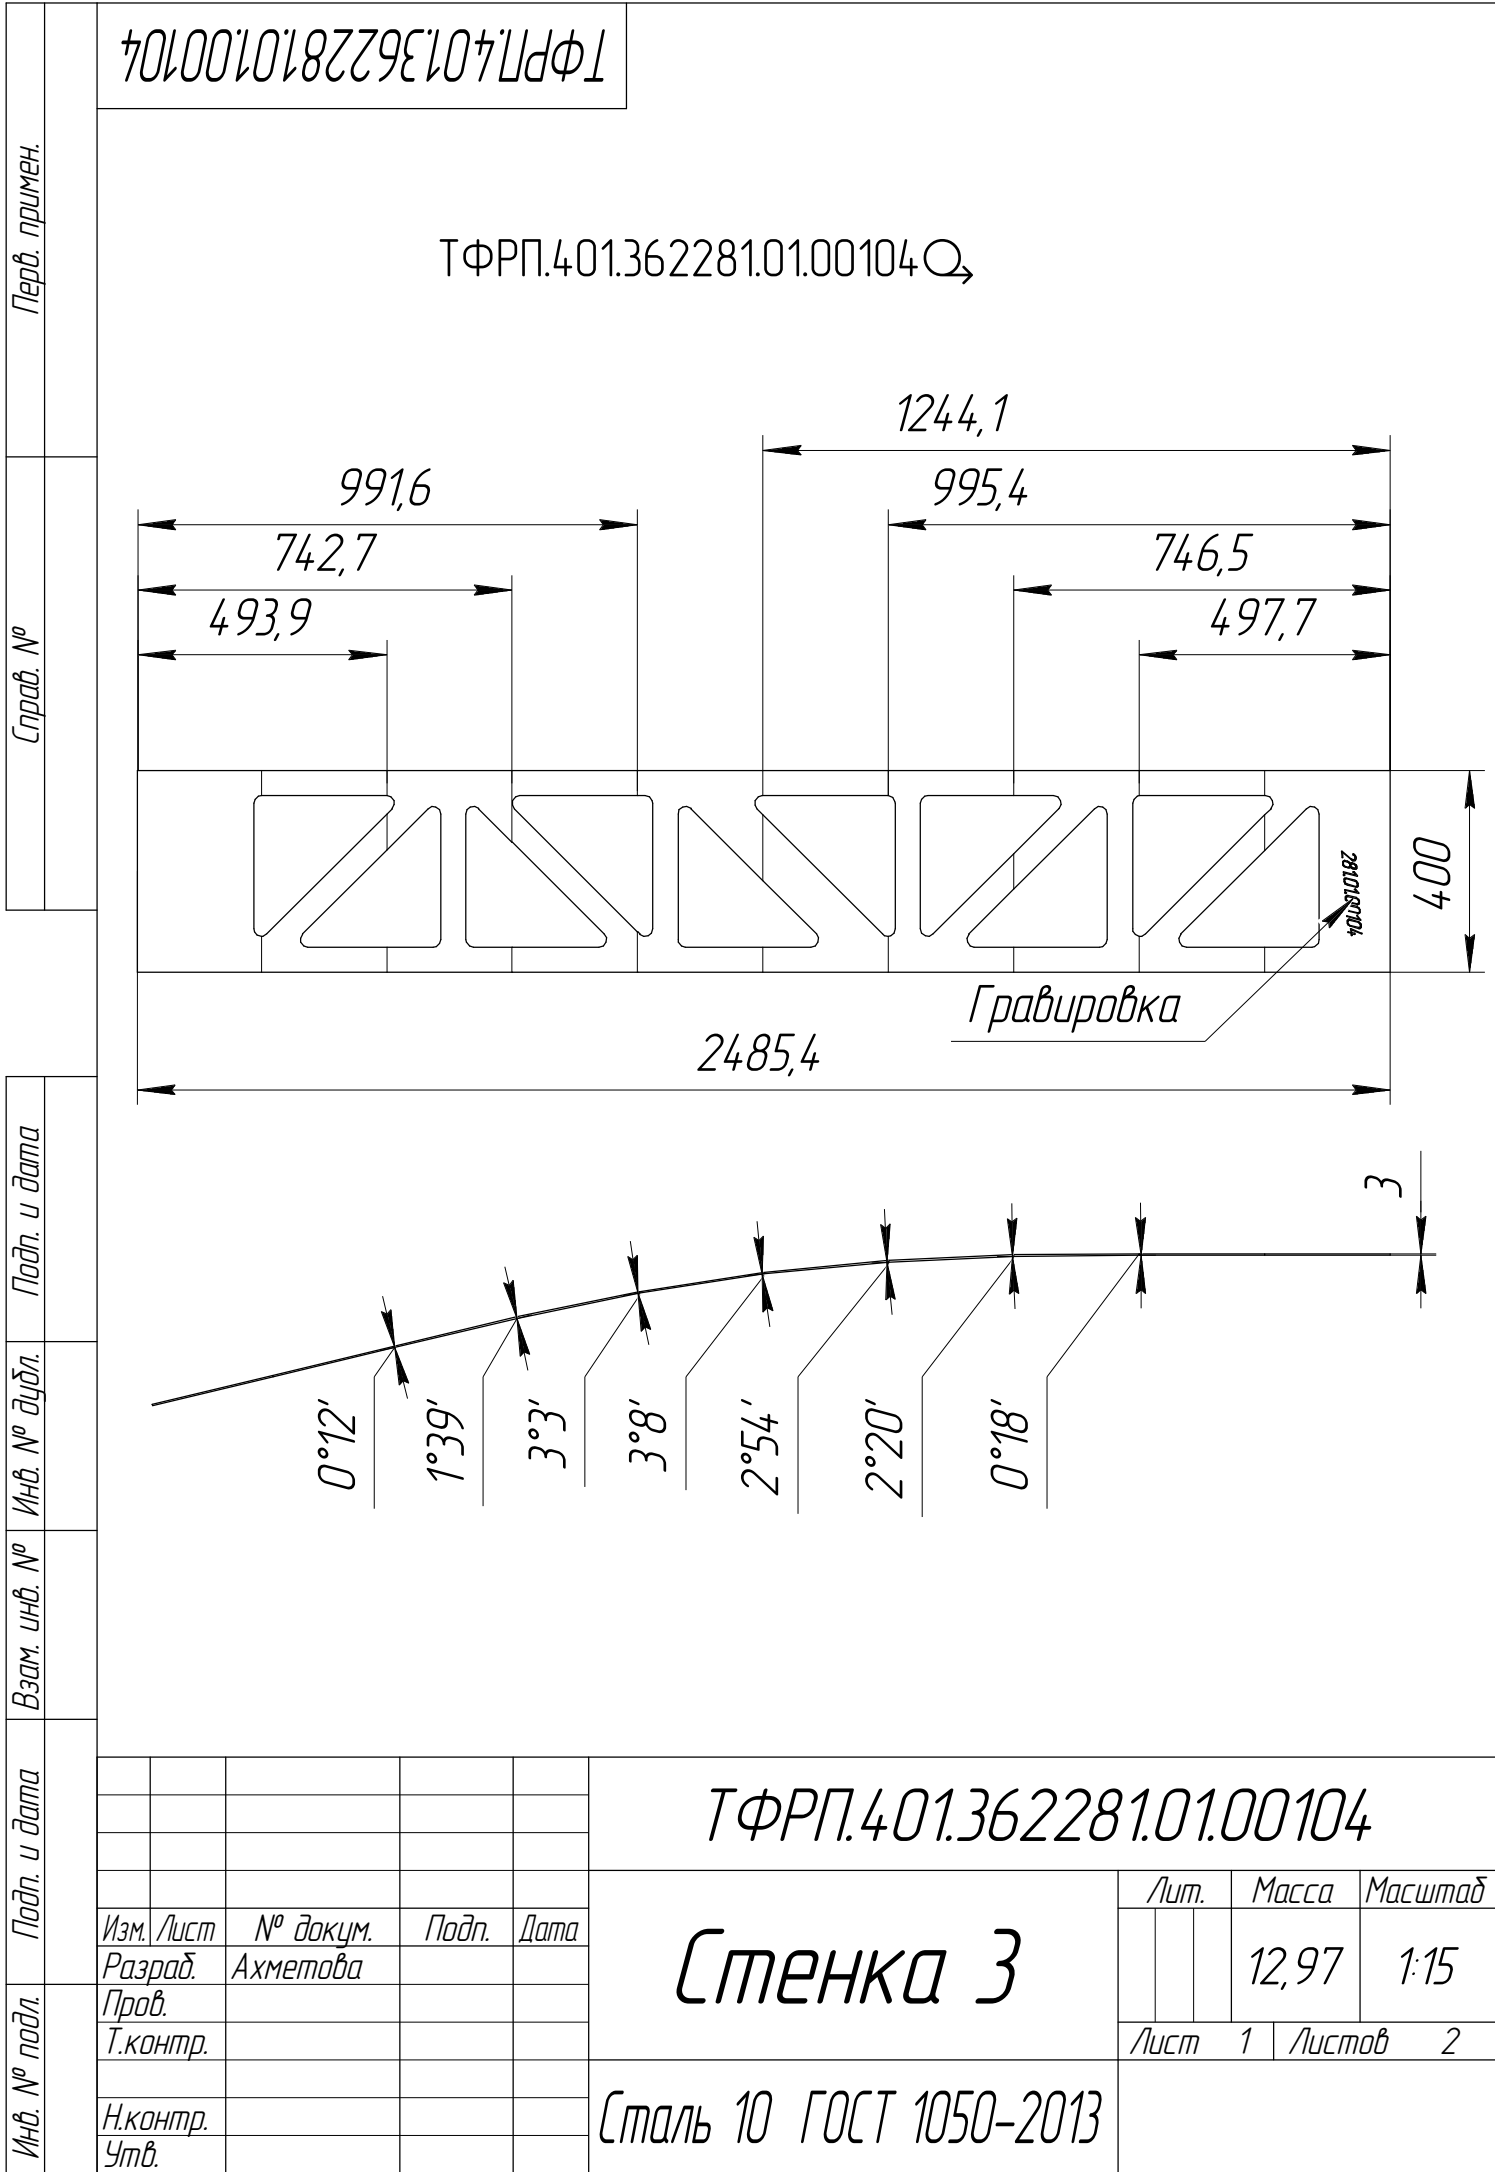

ТФРП.401.362281.01.00104

ТФРП.401.362281.01.00104-01 – зеркальное отражение

Остальное – см. ТФРП.401.362281.01.00104 Q, Y

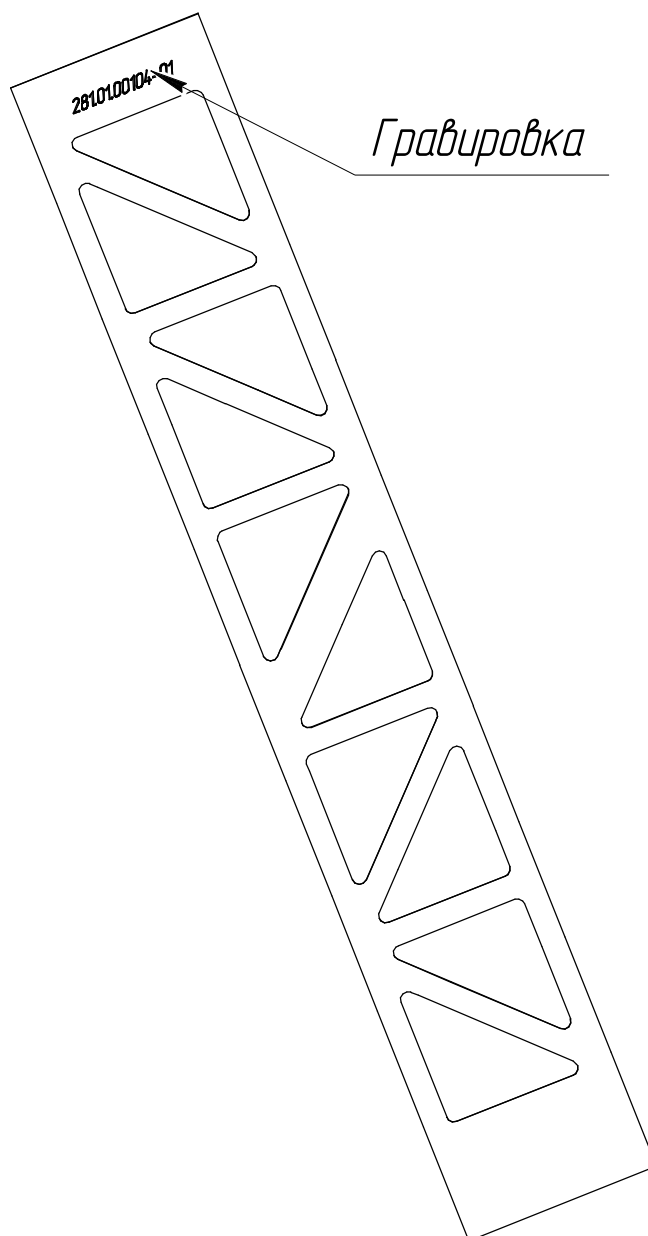


Инв. № подл.	Подп. и дата	Взам. инв. №	Инв. № дубл.	Подп. и дата	ТФРП.401.362281.01.00104					Лист
										2
Изм.	Лист	№ докум.	Подп.	Дата						
Копировал					Формат А4					

Справ. №		Перв. примен.	
Инв. № подл.		Подп. и дата	
Т.контр.		Инв. № докл.	
Н.контр.		Взам. инв. №	
Утв.		Подп. и дата	
Изм. Лист		№ докум.	
Разраб.		Ахметова	
Пров.		Подп.	
Т.контр.		Дата	
Н.контр.			
Утв.			
ТФРП.401.362281.01.00105			
ТФРП.401.362281.01.00105			
1452,1			
Гравировка			
2810100105			
1377,8			
60			
3			
ТФРП.401.362281.01.00105			
Фланец			
Сталь 10 ГОСТ 1050-2013			
Лист 1			
Масса 5,32			
Масштаб 1:15			
Листов 2			
Копировал			
Формат А4			

*TφPΠ4013622810100105*

ТФРП.401.362281.01.00105-01 – зеркальное отражение

Остальное – см. ТФРП.401.362281.01.00105

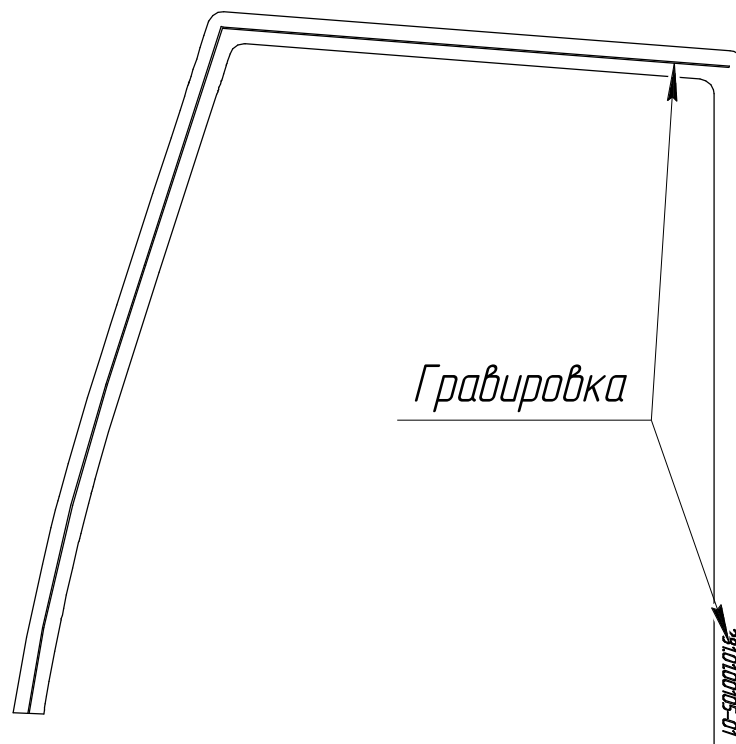


Инв. № подл.	Подп. и дата	Взам. инв. №	Инв. № дудл.	Подп. и дата	<div>28101.00105-01</div>
Изм.	Лист	№ докум.	Подп.	Дата	<div>ТФРП.401.362281.01.00105</div>

Инв. № подл.		Т.контр.		Изм. Лист		Разраб.		Пров.		Н.контр.		Утв.		Инв. № докл.		Взам. инв. №		Справ. №		Перв. примен.	

ТФРП.401.362281.01.00105.01

ТФРП.401.362281.01.00105.01-01 – зеркальное отражение

Остальное – см. ТФРП.401.362281.01.00105.01

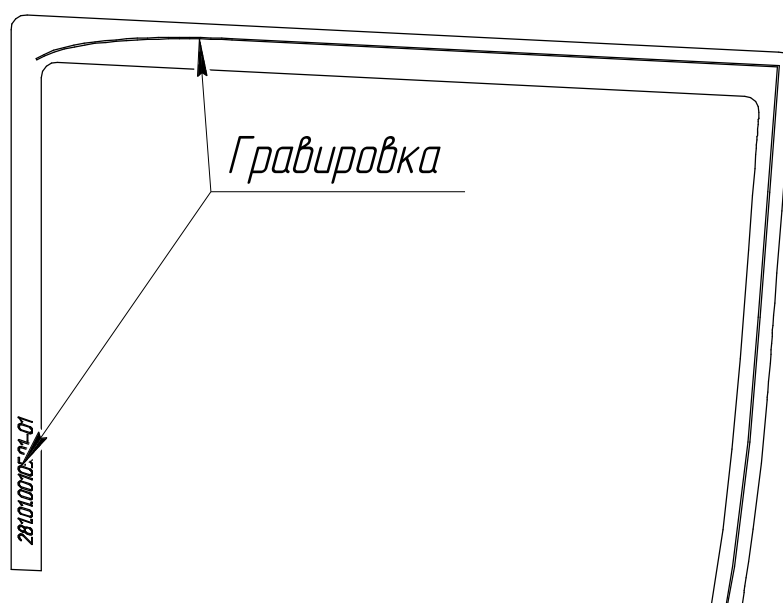

Инв. № подл.	Подп. и дата	Взам. инв. №	Инв. № дубл.	Подп. и дата
Изм.	Лист	№ докум.	Подп.	Дата
ТФРП.401.362281.01.00105.01				
Копировал				Лист
Формат А4				2





ТФРП.401.362281.01.00106

ТФРП.401.362281.01.00106-01 – зеркальное отражение

Остальное – см. ТФРП.401.362281.01.00106Q,

Гравировка



Инв. № подл.	Подп. и дата	Взам. инв. №	Инв. № дудл.	Подп. и дата

Изм.	Лист	№ докум.	Подп.	Дата

ТФРП.401.362281.01.00106

Лист
2

Копировал

Формат А4